
Архитектурно заснемане

Ателие, Овча купел

46.4 кв.м

Нсв = 260

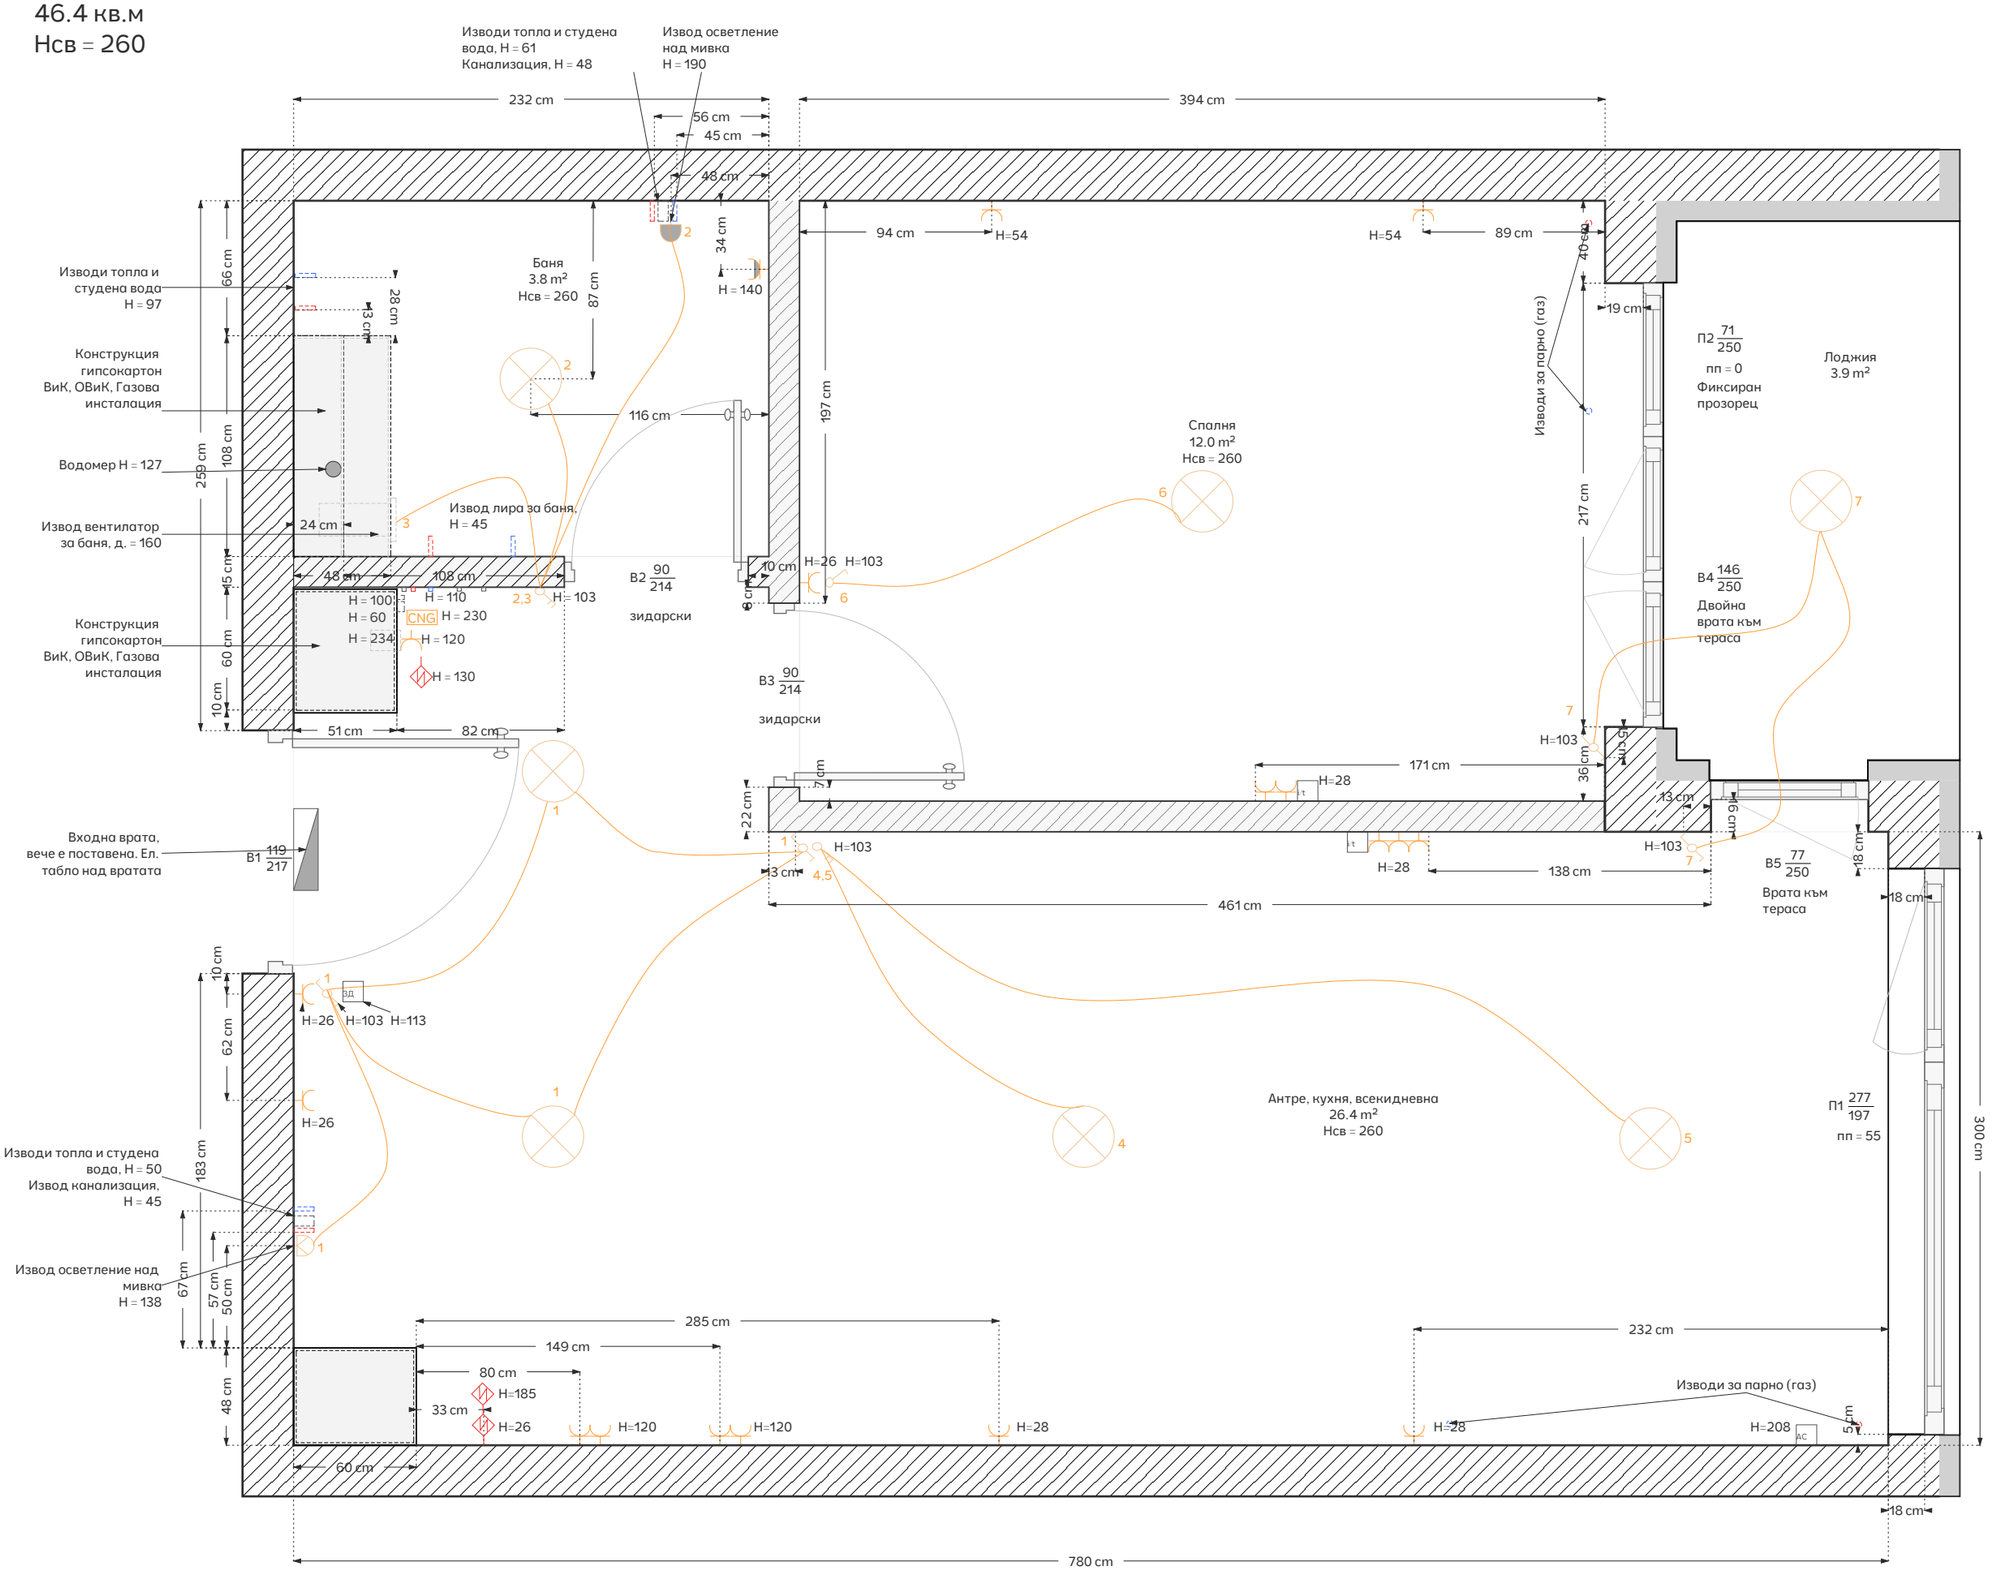

+359 898 24 82 85
contact@stelapopova.com
www.stelapopova.com

Drawing name :
Архитектурно заснемане

Project name :
Ателие Алера 2

Project notes :

Drawing No : A01

Date : 29/09/2026

Scale : 1:30


Made by : Стела Попова

Разпределение

Ателие Алера 2, Овча купел

46.4 кв.м

Нсв = 260

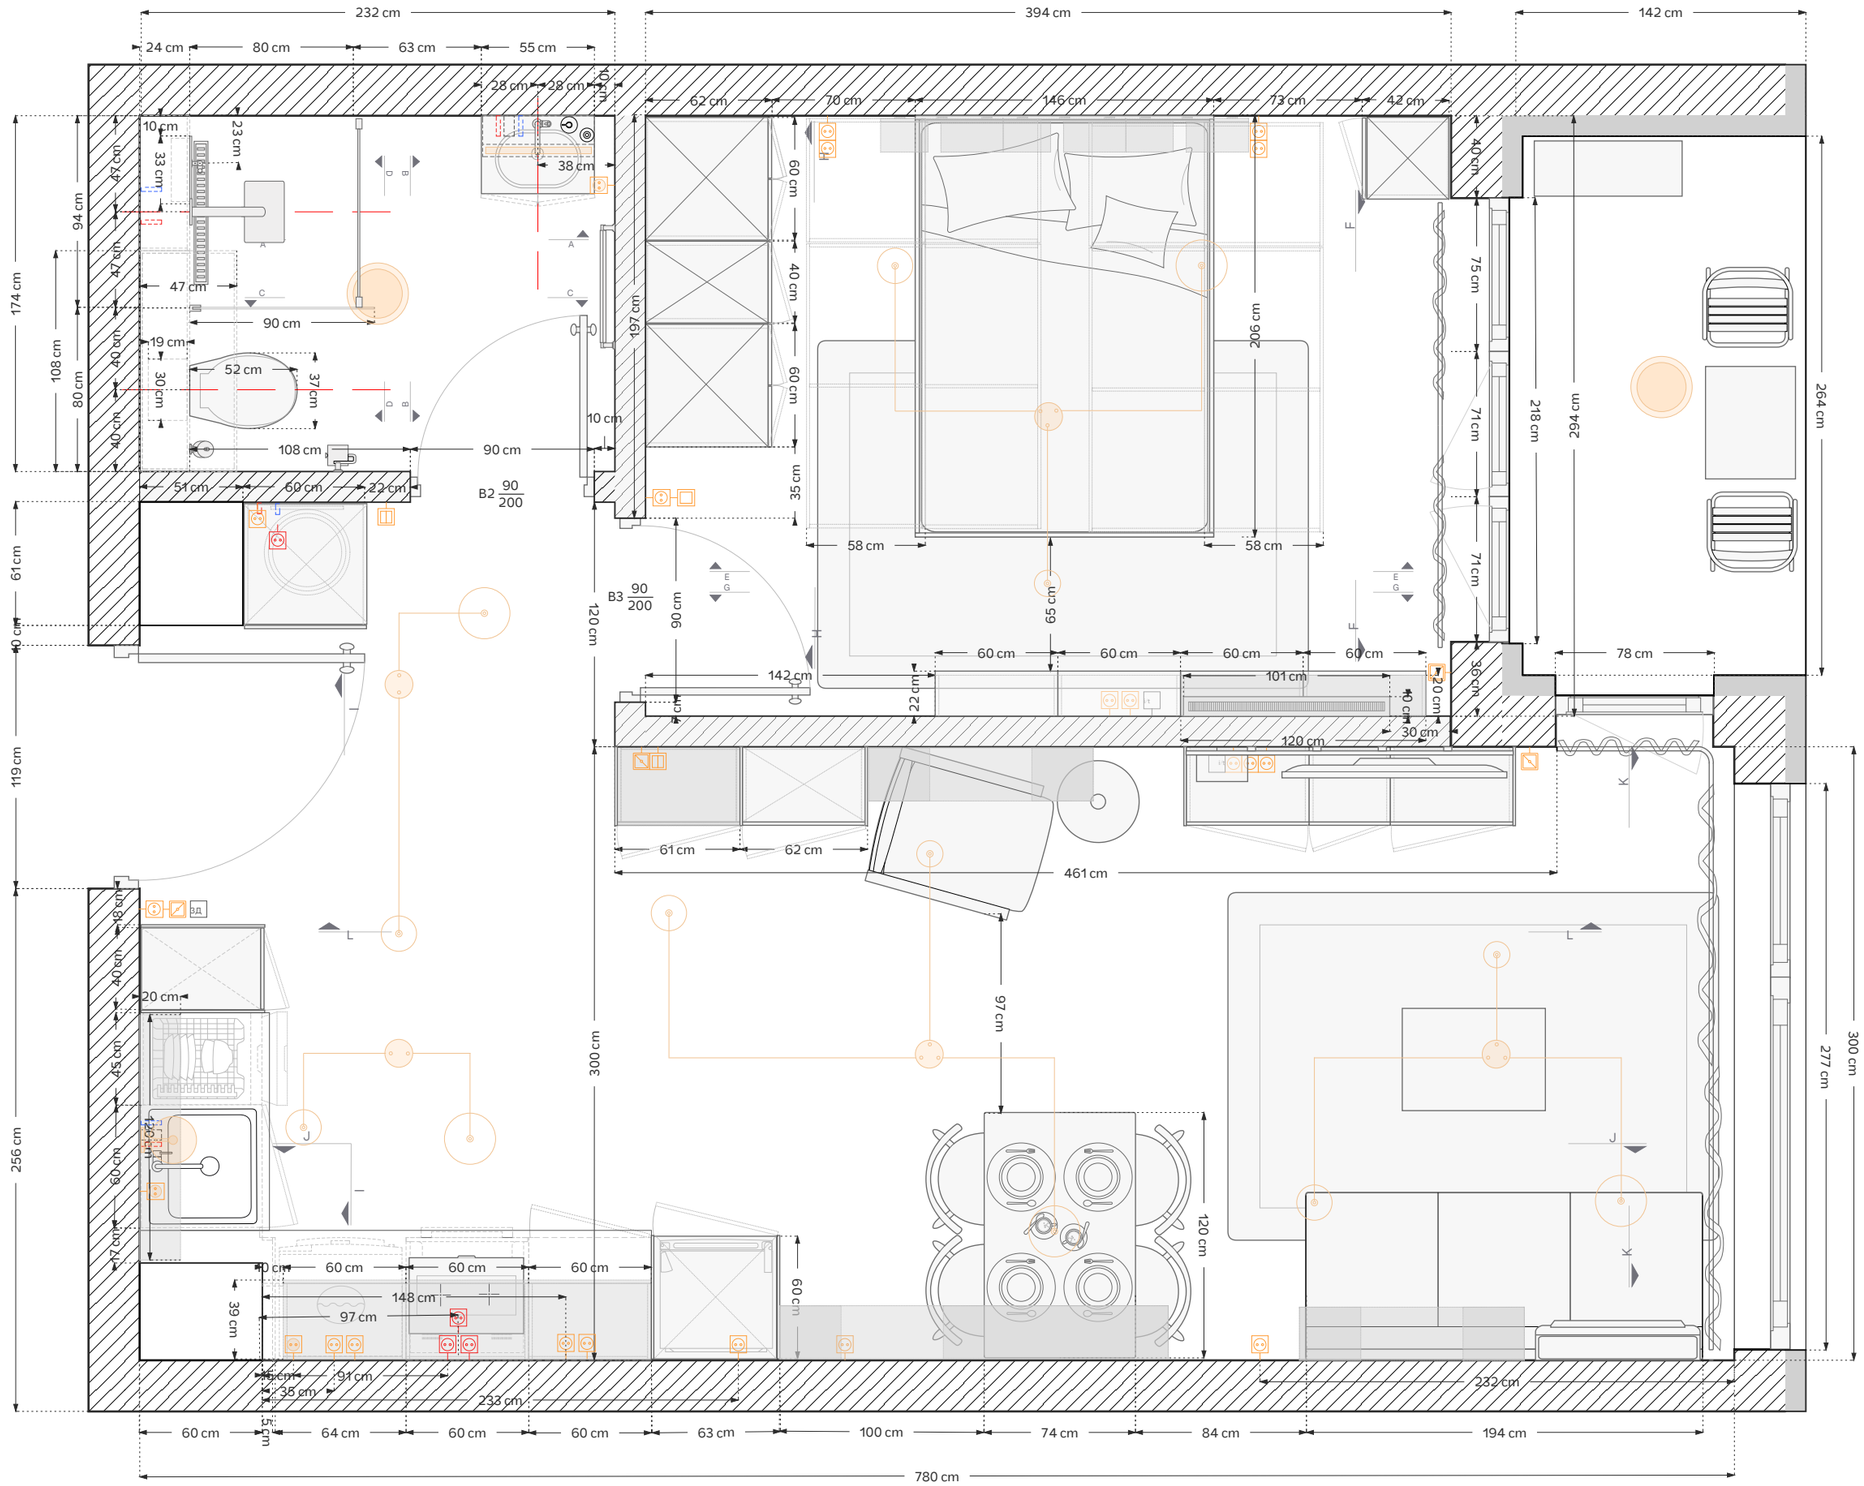

SP interior design

+359 898 24 82 85
contact@stelapopova.com
www.stelapopova.com

Drawing name :

Разпределение

Project name :

Ателие Алера 2

Project notes :


Drawing No :	Date :
A02	29/09/2026
Scale :	Made by :
1:30	Стела Попова

Изграждане, промени ВиК, ОВиК, Ел. Инсталация

Ателие, Овча купел

46.4 кв.м

Нсв = 260

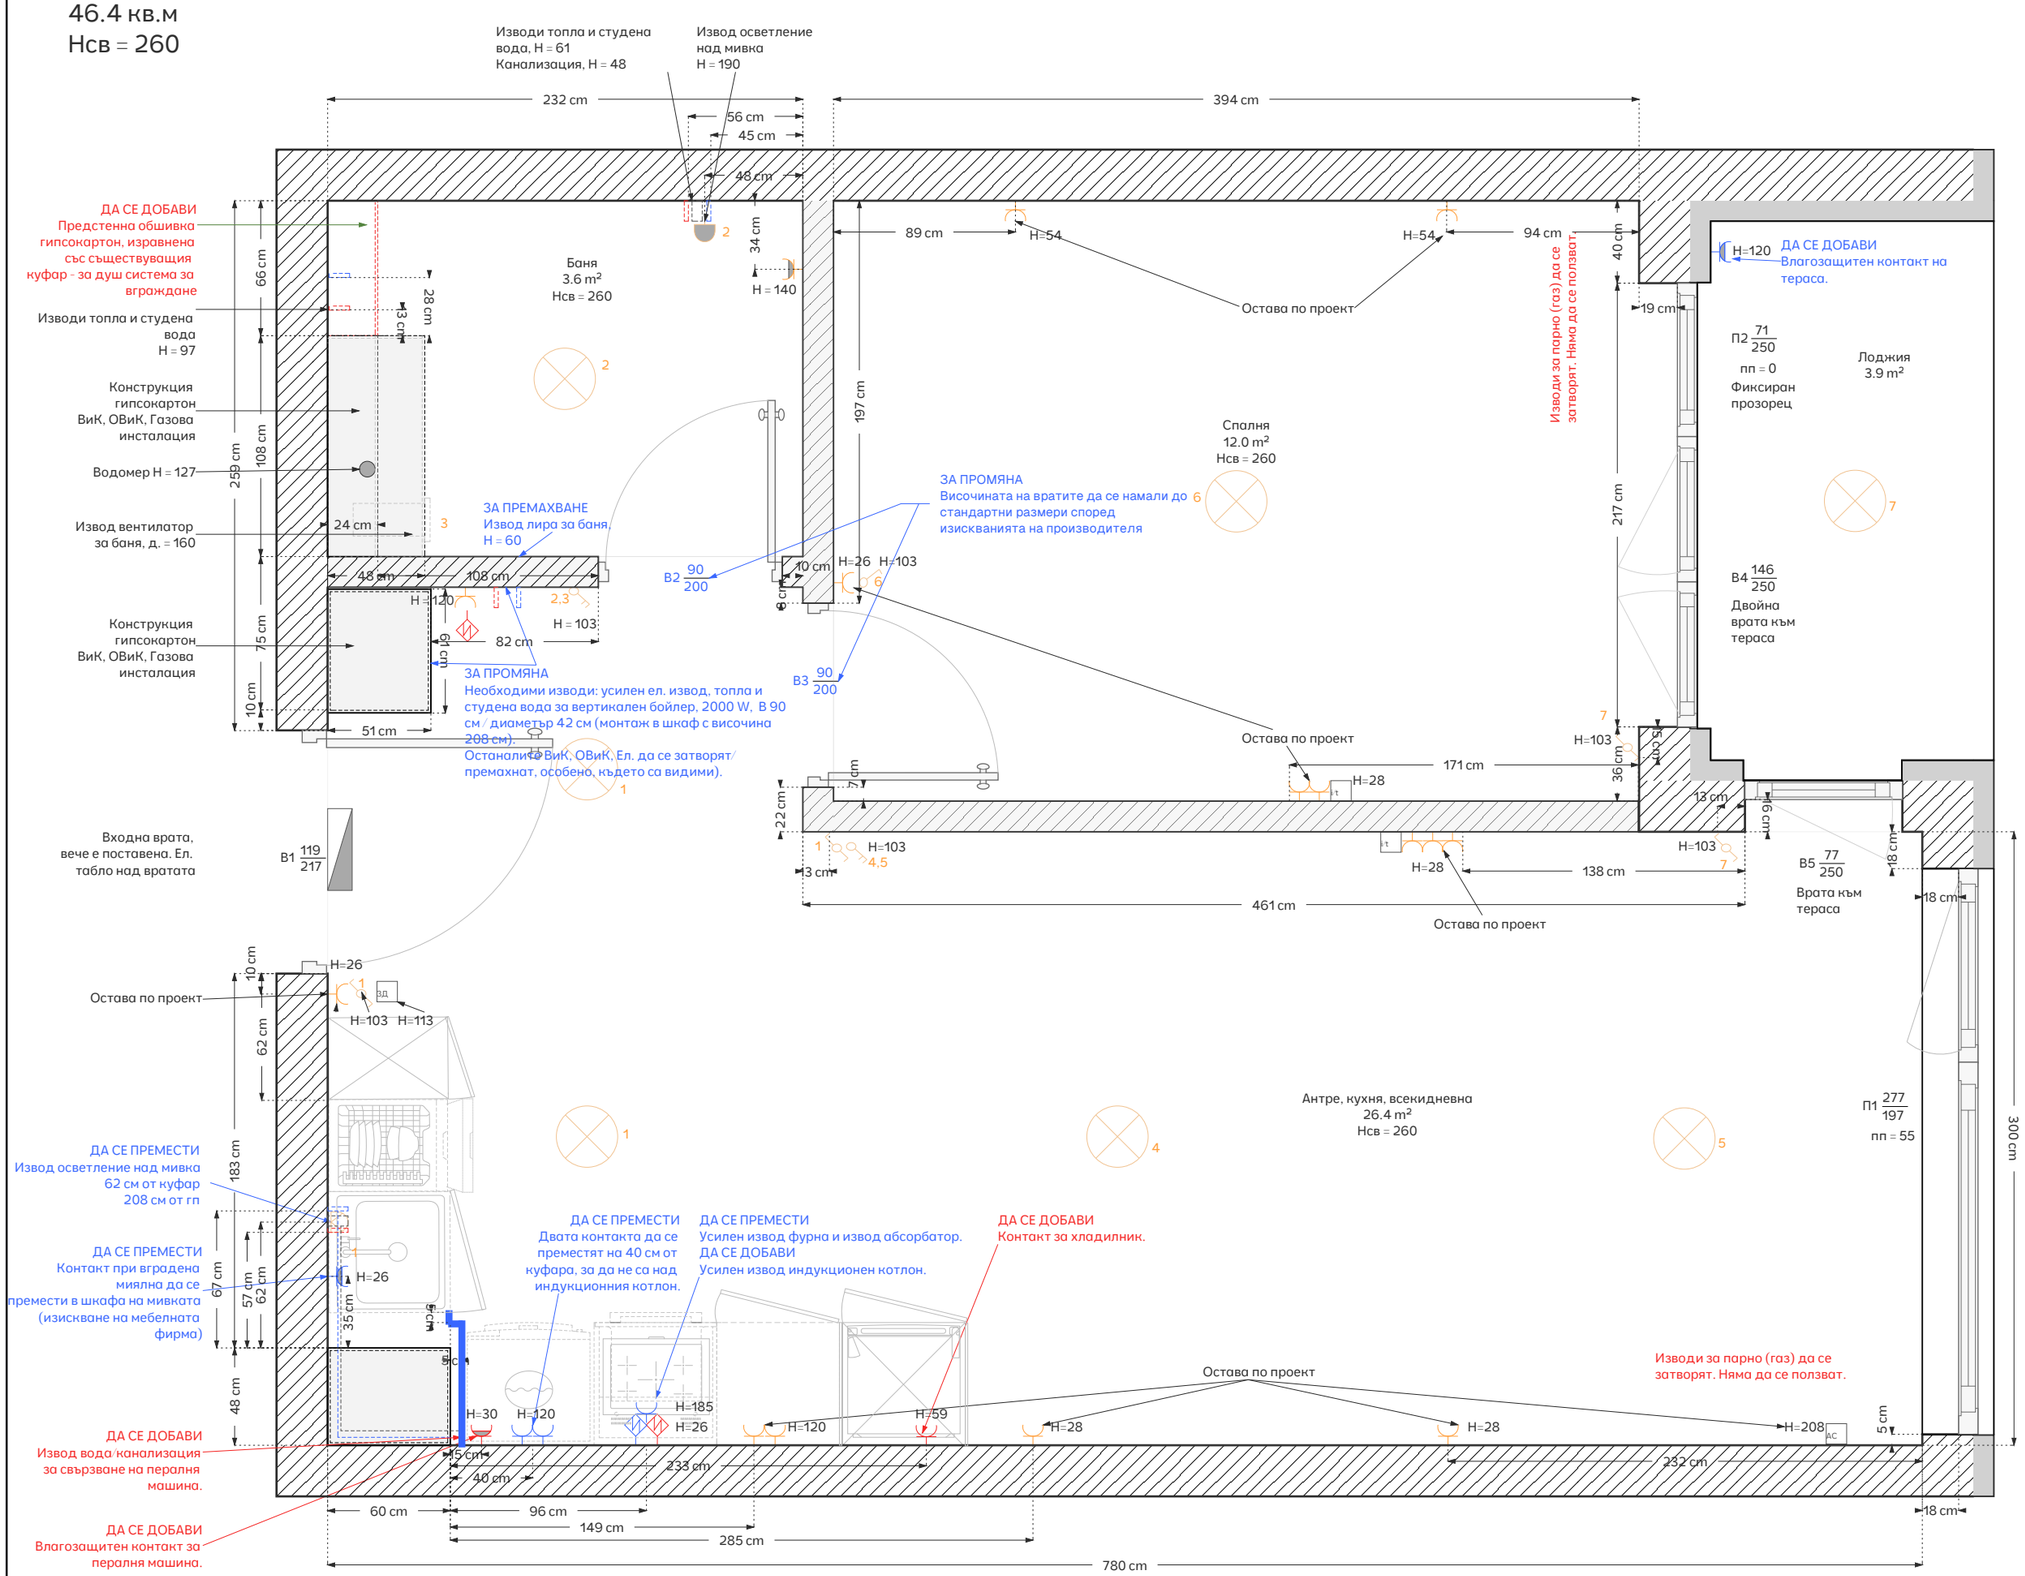

interior design

+359 898 24 82 85
contact@stelapopova.com
www.stelapopova.com

Drawing name :
Промени

Project name :
Ателие Алера 2

Project notes :

Drawing No : A03

Date : 29/09/2026

Scale : 1:30


Made by : Стела Попова

Настилки

Ателие Алера 2, Овча купел

46.4 кв.м

Нсв = 260

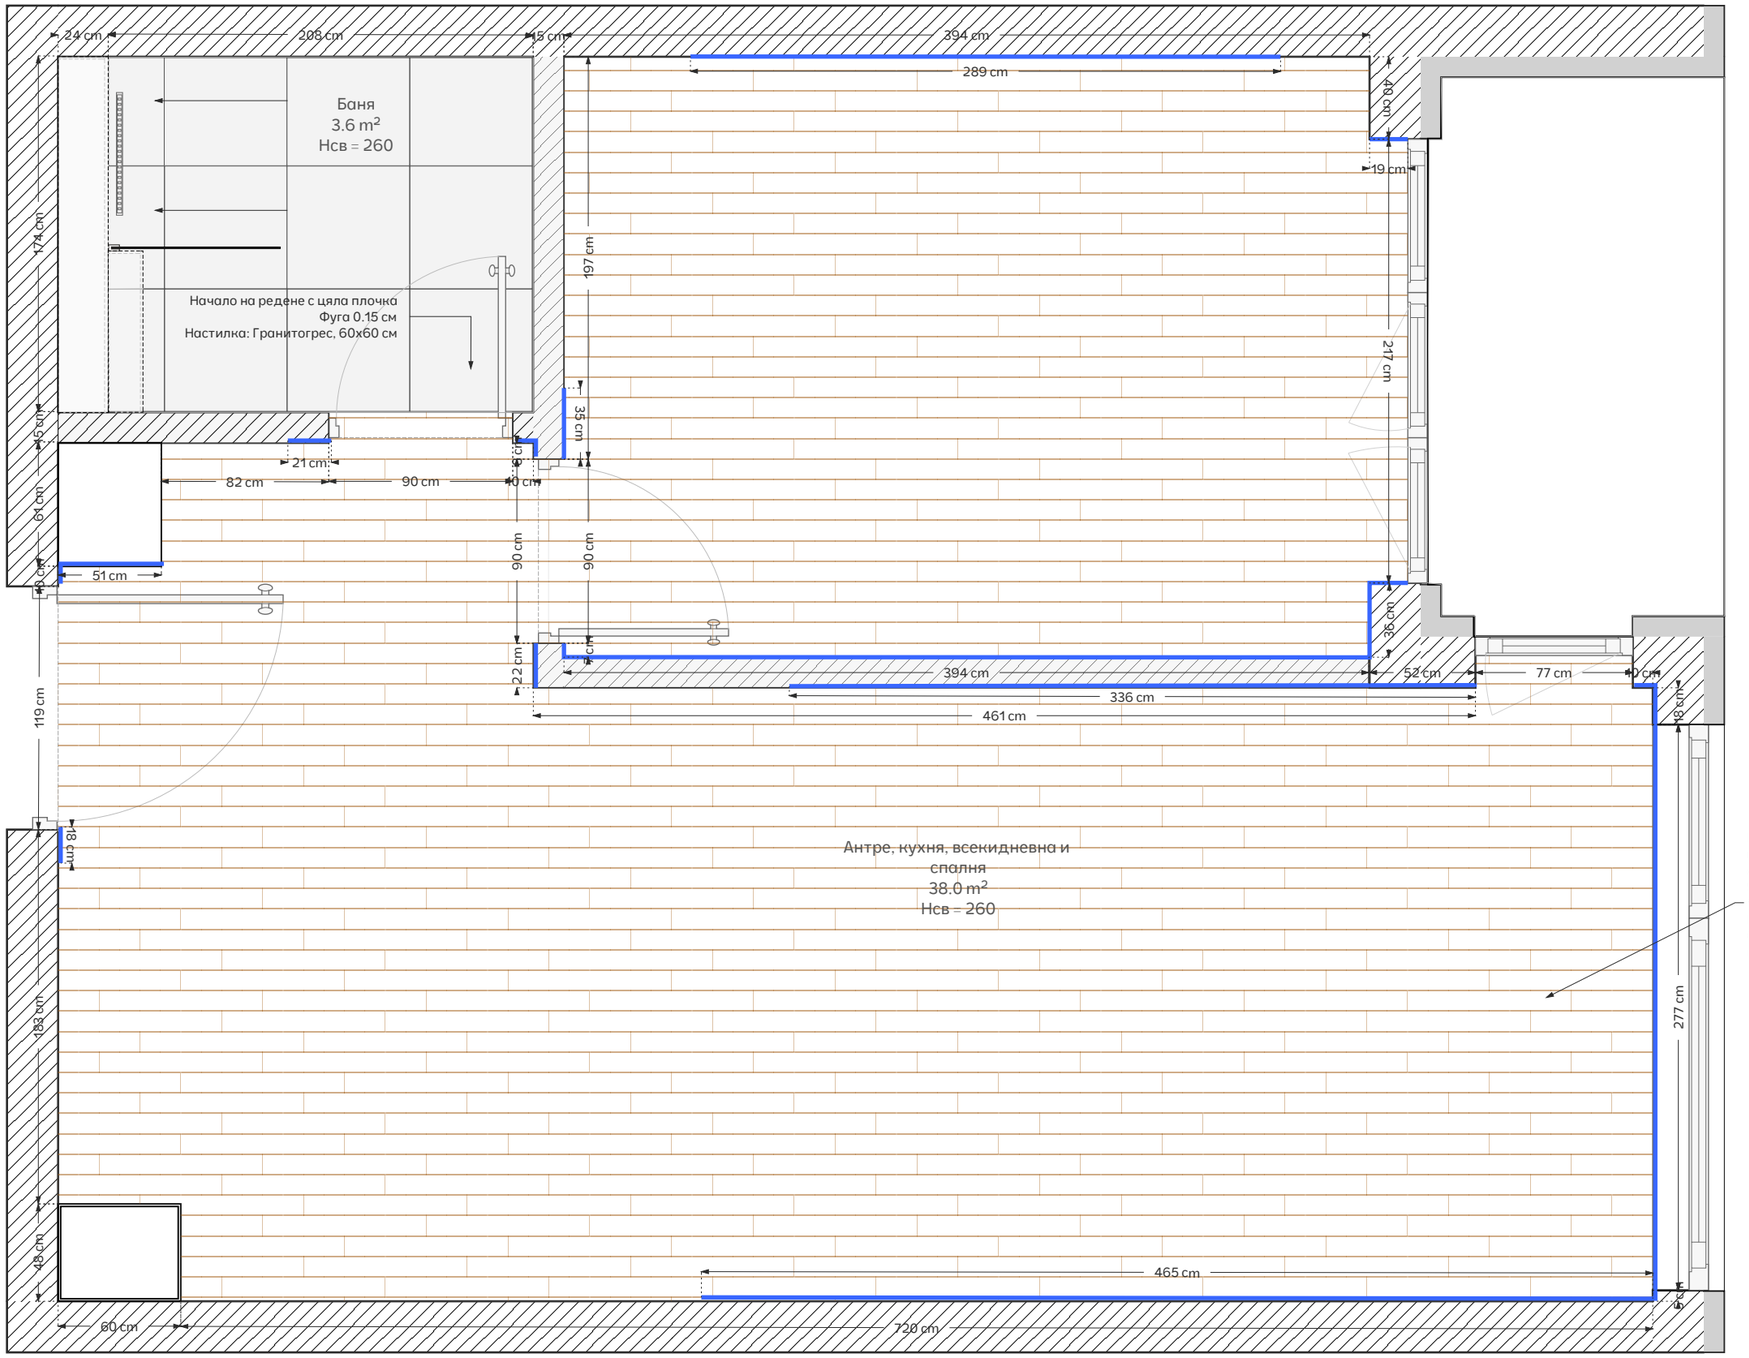

Настилка антре, кухня, всекидневна, спалня
SPC Zeno Oak
1234x198x5mm,
PF3000009,
Class 33, вградена подложка

Материали

Гранитогрес (под баня)
60х60 см
3.6 кв.м

SPC Zeno Oak
1234x198x5mm
Class 33
вградена подложка,
38 кв.м

Подов перваз
за поставяне след корпусна мебел. Конкретният продукт да се доуточни
21 л. м

SP interior design

+359 898 24 82 85
contact@stelapopova.com
www.stelapopova.com

Drawing name :
Настилки

Project name :
Ателие Алера 2

Project notes :

Drawing No :
A04

Date :
29/09/2026

Scale :
1:30

Made by :
Стела Попова


Разгъвки баня

Ателие Алера 2, Овча купел


46.4 кв.м


Нсв = 260

A-A

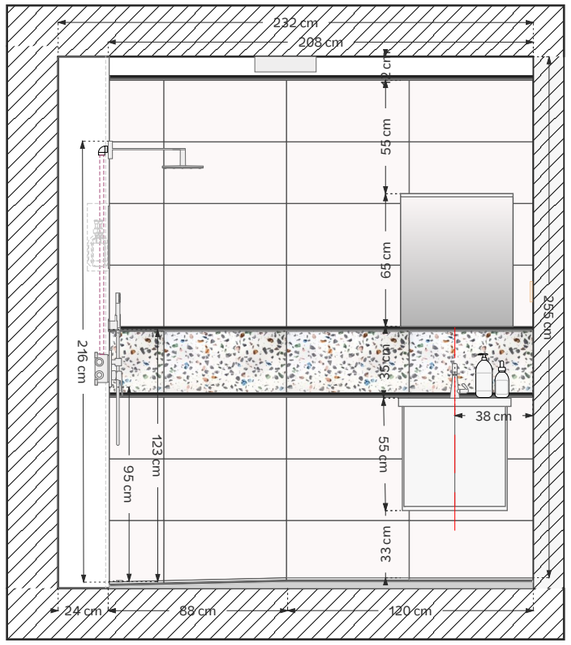


B-B

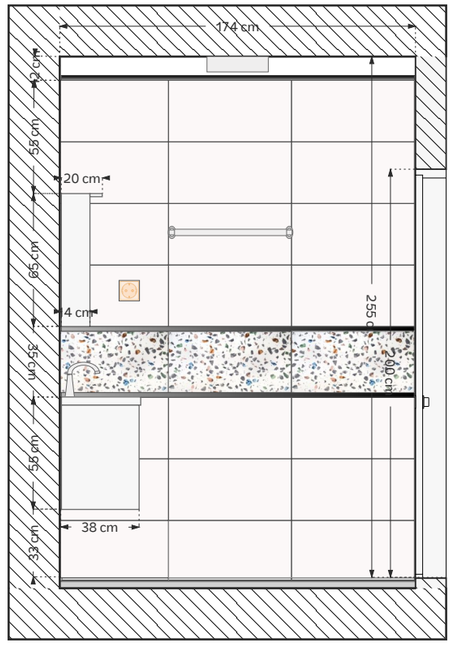


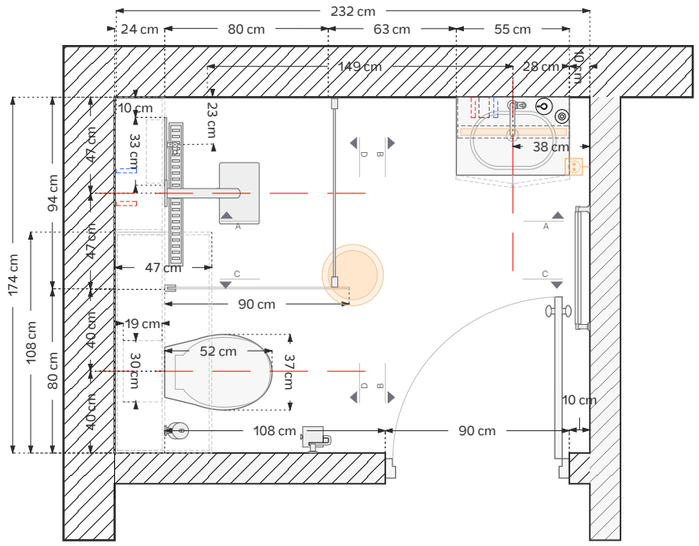


C-C

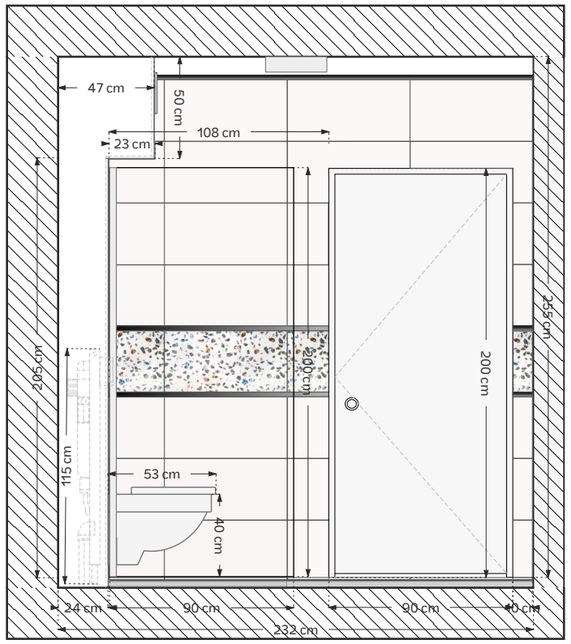

D-D

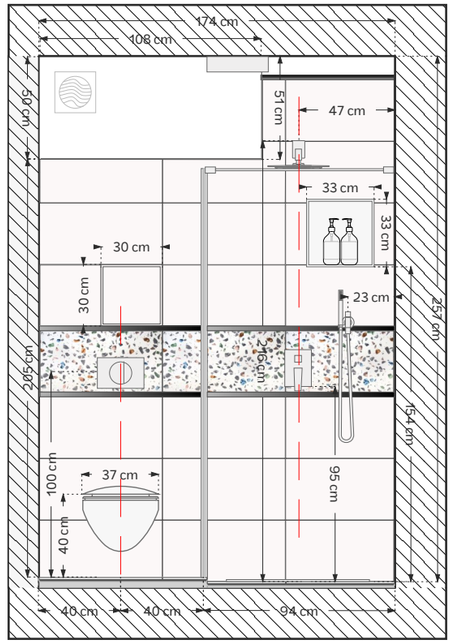

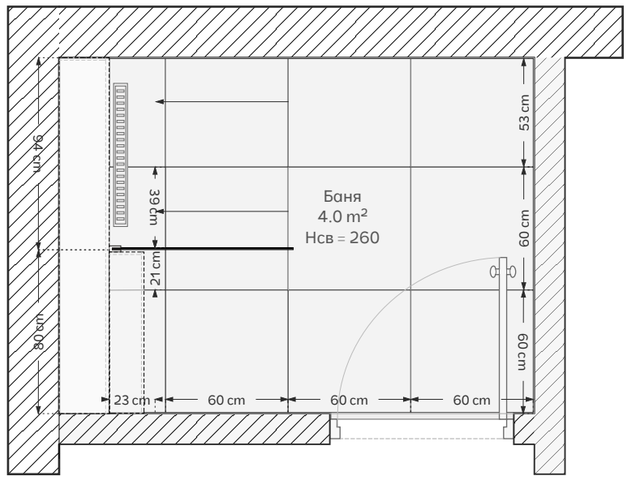

+359 898 24 82 85
contact@stelapopova.com
www.stelapopova.com

Drawing name :
Разгъвки Баня - интериор


Project name :
Ателие Алера 2

Project notes :

Drawing No :	Date :
A05	29/09/2026
Scale :	Made by :
1:30	Стела Попова







Ателие Алера 2, Овча купел
46.4 кв.м
Нсв = 260

A-A

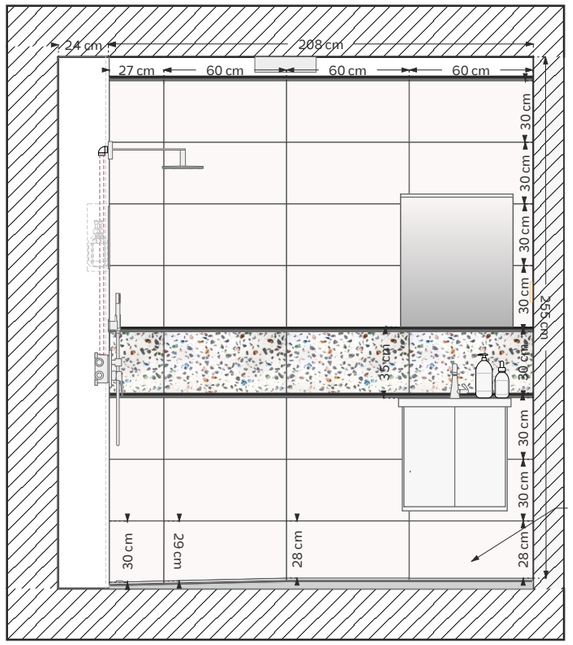
24 cm
208 cm
27 cm
60 cm
60 cm
60 cm
30 cm
30 cm
30 cm
30 cm
255 cm
35 cm
30 cm
30 cm
30 cm
30

Баня - обзавеждане

Ателие Алера 2, Овча купел
46.4 кв.м
Нсв = 260

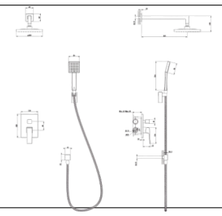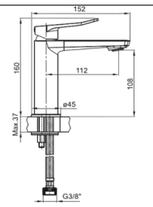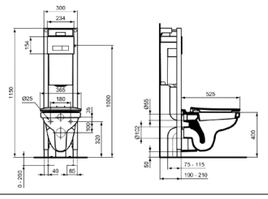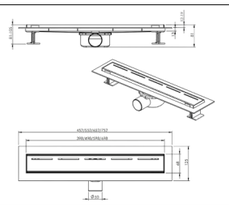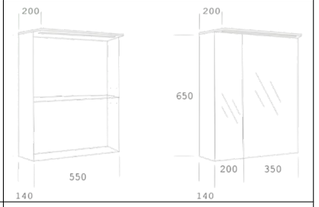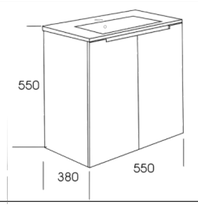Продукт	Снимка	Информация на производителя	Продукт	Снимка	Информация на производителя
Душ система за вграждане Месингов смесител за вграждане с превключвател Месингово рамо Квадратна душ пита 20,3*20,3 см С подвижен душ, шлаух и държач Цвят: хром			Смесител за мивка		
Структура за вграждане и тоалетна			Лампа за баня CLEO 2xE27/24W/230V Ø 30 см бяла IP54		
Стационарен параван Прозрачно закалено стъкло: 8мм Хром профил стена – стъкло Силиконово уплътнение под – стъкло Телескопично квадратно рамо 70-120см Компенсаторен профил до +2см Размери: 90x200 см			Аксесоари	да се уточнят допълнително	да се уточнят допълнително
Ревизионна врата за плочка 30x30			Линеен сифон Регулируема височина:70-95мм Изход: DN50 Дебит:52л/мин Система:Magnet dry & Wet Въртящ се дизайн Мокър и сух затвор Размер: 6,8*8,10*70		
Вентилатор за баня ДИАМЕТЪР : 100 mm ДЕБИТ : 180 м3/ч НИВО НА ШУМ : 30 dB ЦВЯТ : БЯЛ КЛАПА			Горен шкаф за мивка		
					

SP interior design
+359 898 24 82 85
contact@stelapopova.com
www.stelapopova.com

Drawing name :
Баня - обзавеждане

Project name :
Ателие Алера 2

Project notes :

Drawing No : A10
Date : 29/09/2026
Scale : 1:30
Made by : Стела Попова


Разгъвки спалня

Ателие Алера 2, Овча купел


46.4 кв.м

Нсв = 260


E-E

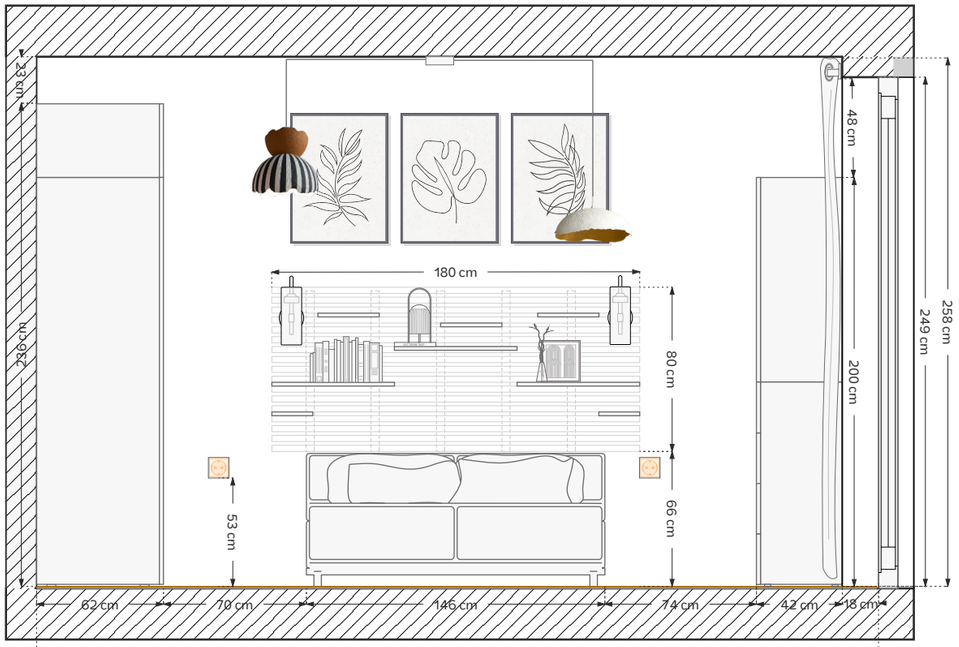


H-H

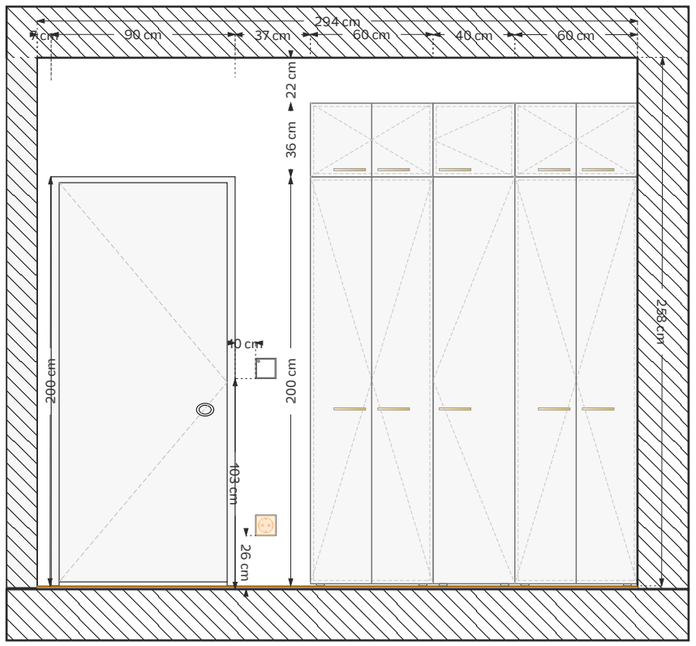

G-G

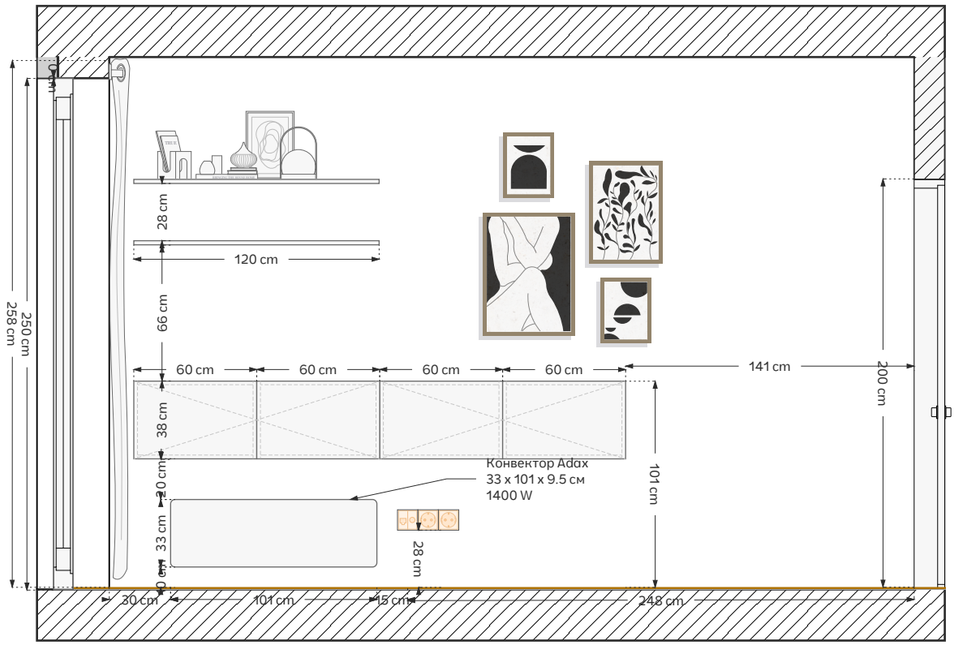

F-F

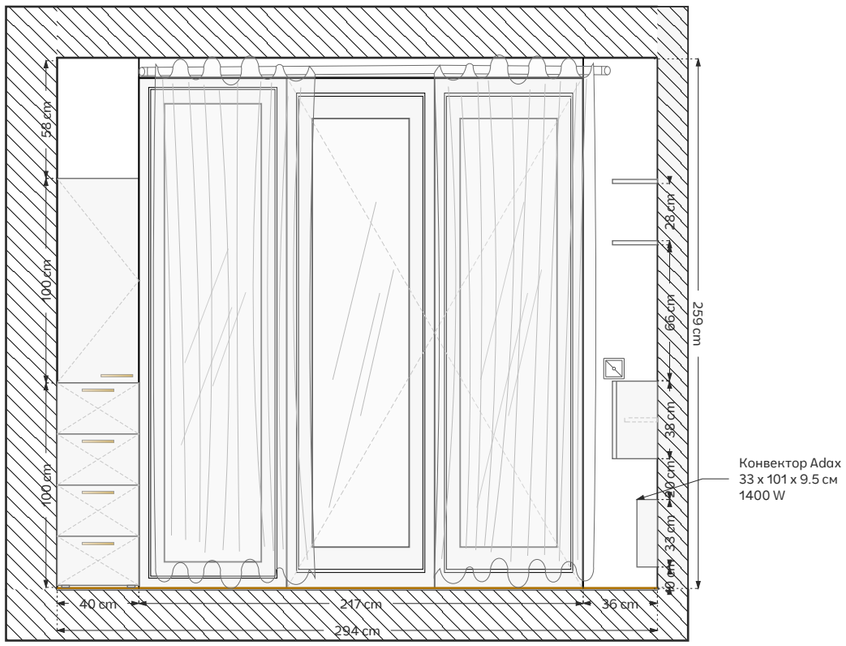

SP interior design

+359 898 24 82 85

contact@stelapopova.com

www.stelapopova.com

Drawing name :

Разгъвки спалня

Project name :

Ателие Алера 2

Project notes :

Drawing No :	Date :
A07	29/09/2026
Scale :	Made by :
1:30	Стела Попова


Разгъвки антре, кухня, хол

Ателие Алера 2, Овча купел

46.4 кв.м

Нсв = 260

K-K

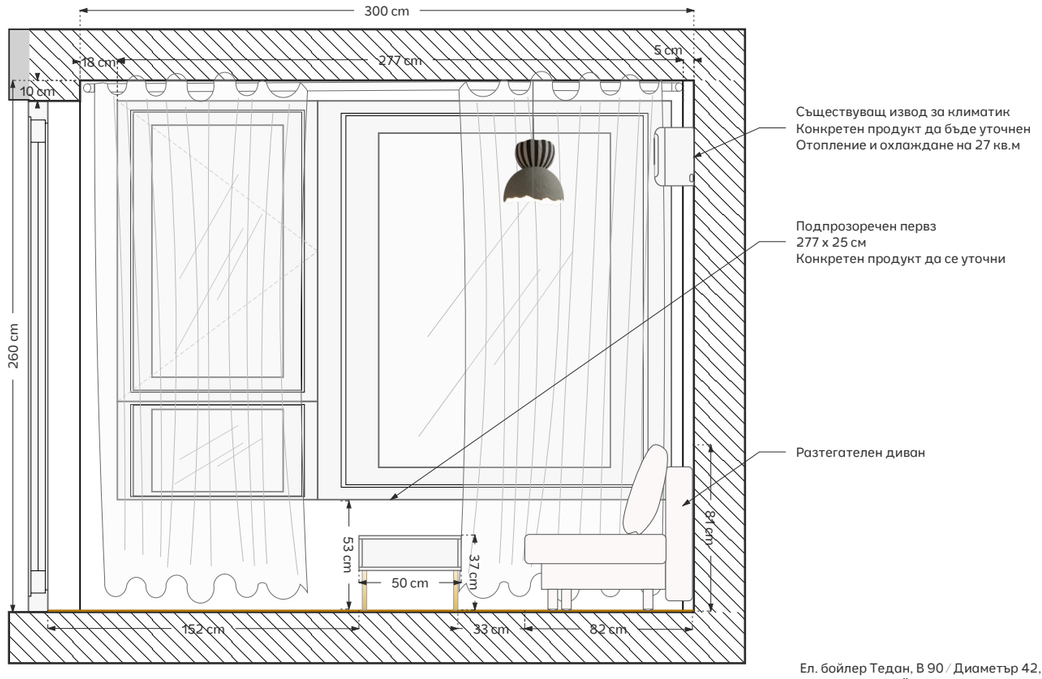


Съществуващ извод за климатик
Конкретен продукт да бъде уточнен
Отопление и охлаждане на 27 кв.м

Подпрозоречен первз
277 x 25 см
Конкретен продукт да се уточни

Разтегателен диван

Ел. бойлер Тедан, В 90 / Диаметър 42, 80 л, 2000 W,
изводи вода 1/2'',вертикален монтаж във висок шкаф
Необходими изводи за топла и студена вода
(такива са изведени по проект за газов бойлер)
и усилен ел. извод на самостоятелен кръг
(по проект е изкаран извод за газов бойлер, мощност 1000 W)

L-L

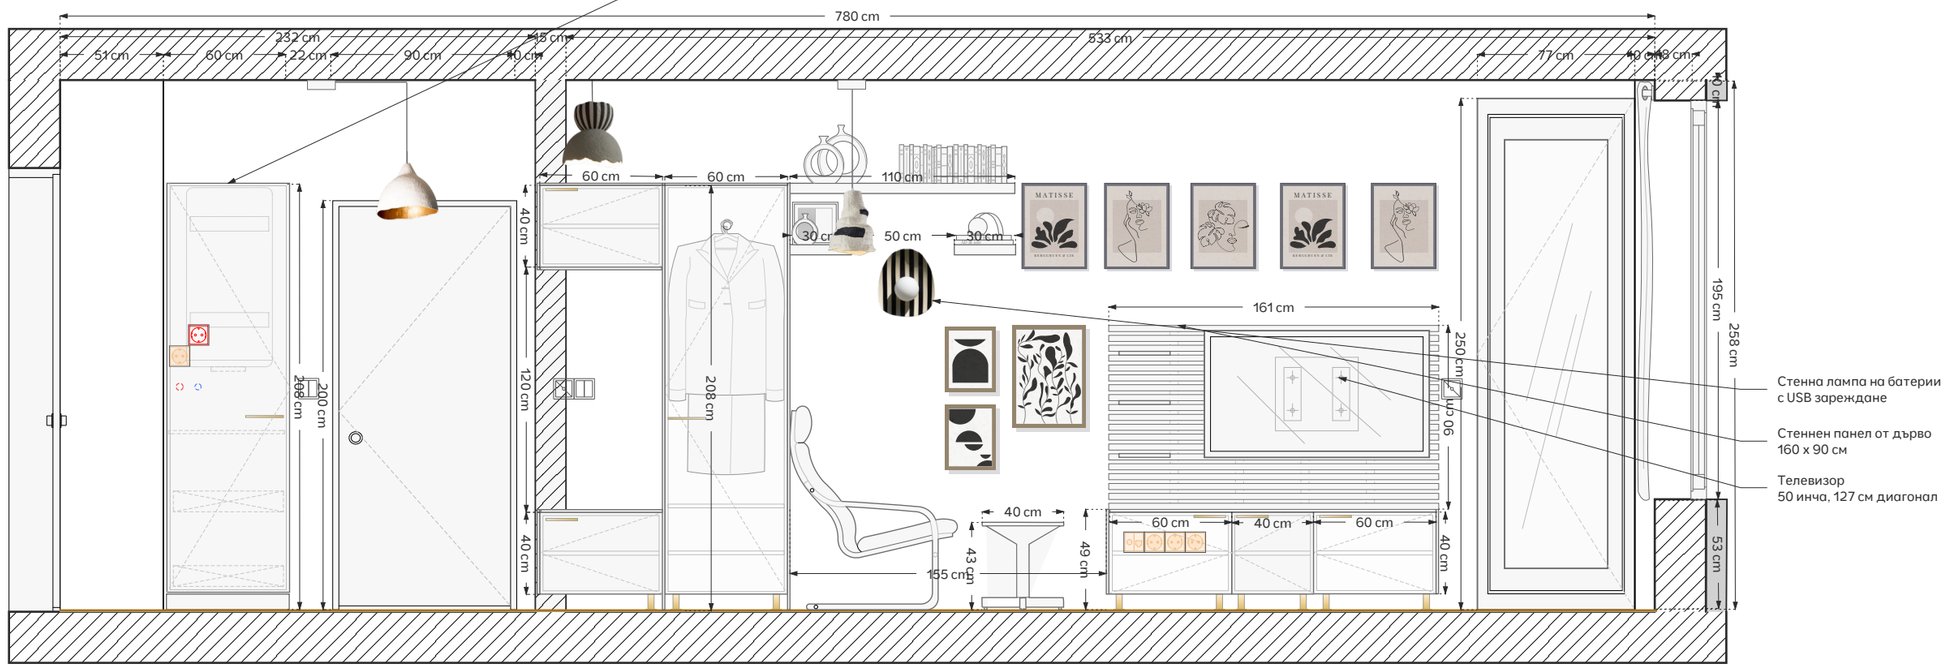

Стенна лампа на батерии
с USB зареждане

Стеннен панел от дърво
160 x 90 см

Телевизор
50 инча, 127 см диагонал

SP interior design

+359 898 24 82 85
contact@stelapopova.com
www.stelapopova.com

Drawing name :

Разгъвки антре кухня
всекидневна
Стени K-K, L-L

Project name :

Ателие Алера 2

Project notes :

Drawing No :	Date :
A09	29/09/2026
Scale :	Made by :
1:30	Стела Попова


Разгъвки антре, кухня, хол

Ателие Алера 2, Овча купел

46.4 кв.м

Нсв = 260

J-J

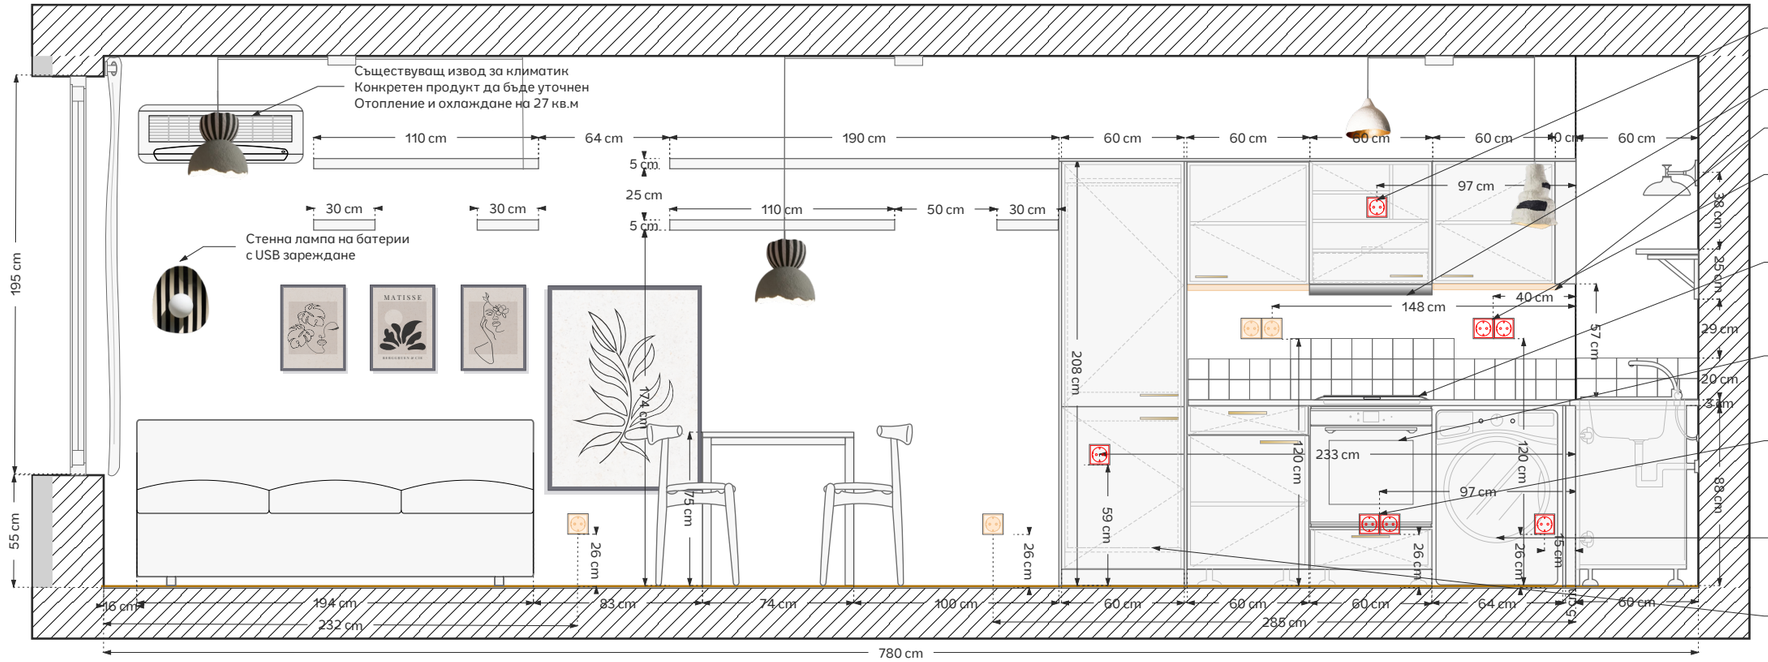

Съществуващ извод за абсорбатор, да се премести на 97 см от куфара.

Телескопичен абсорбатор за вграждане с въглен филтър за рециркулация на въздуха и LED осветление

LED осветление за плот с батерии и USB зареждане

Съществуващи контакти
Да се преместят на 40 см от куфар,
за да не бъдат над индукционния котлон

Готварски плот с индукционни зони
Дясно: 15 см - 2000 W. Ляво: 14,5 см – 1200W.
Консумация на енергия: 3200W. Волтаж: 220-240V.
Ампераж: 15А.
Необходимо захранване от минимум 16А.
Препоръчителна твърда връзка.


Фурна (твърда връзка)
Волтаж: 220-240V.
Необходим е предпазител (бушон), минимум 16А.

Съществуващ усилен извод за фурна
Да се премести на 97 см от куфара.
Да се добави усилен извод за индукционен котлон
(виж. спецификациите на котлона:
3200 W, 15A, 220-240 V)

Свободностояща пералня под плот
В куфара трябва да се прекарат от съседната стена
изводи за студена и отпадна вода
за свързване на пералнята
Да се добави влагозащитен контакт за пералня

Хладилник за вграждане
Да се добави контакт

I-I

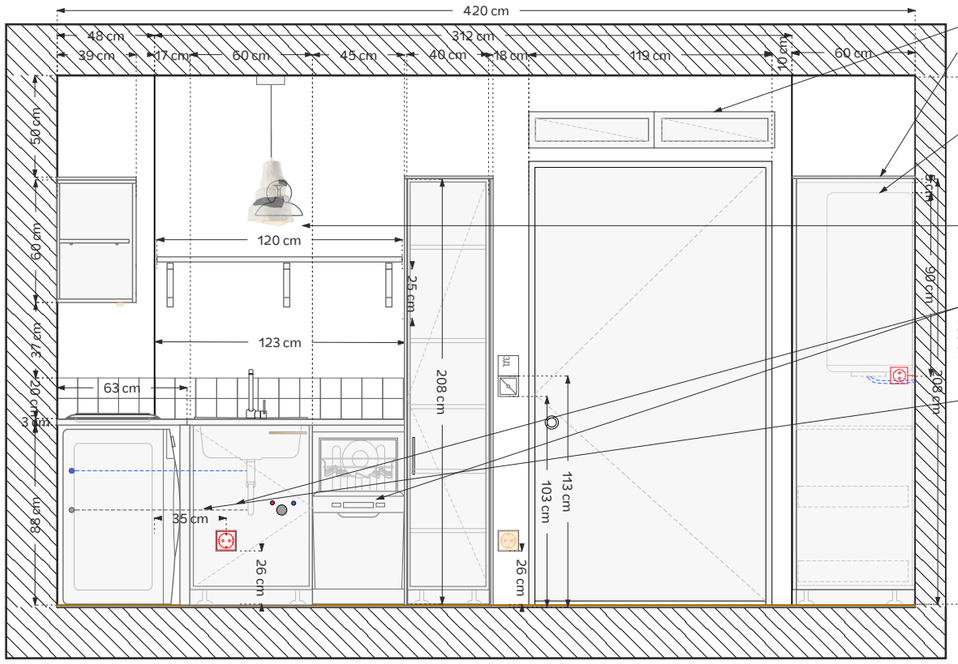

Ел. табло, съществуващо по проект

Висок шкаф

Ел. бойлер Тедан, В 90 / Диаметър 42, 80 л, 2000 W
изводи вода 1/2"
вертикален монтаж във висок шкаф
Необходими изводи за топла и студена вода
(такива са изведени по проект за газов бойлер)
и усилен ел. извод на самостоятелен кръг
(по проект е изкаран извод за газов бойлер, мощност 1000 W)

Съществуващият извод за осветление над мивка
да се премести на 62 см от куфара
и на 208 см от гп

Миялна за вграждане
По проект съществува контакт,
който трябва да бъде преместен в шкафа
на мивката (изискване на мебелната фирма
при такива уреди за вграждане)

Извод канализация и студена вода за свързване на
пералня - да се обсъди, дали може да се прекарат
в съществуващия куфар.

SP interior design

+359 898 24 82 85
contact@stelapopova.com
www.stelapopova.com

Drawing name :
Разгъвки Антре Кухня
Всекидневна
Стени I-I, J-J

Project name :
Ателие Алера 2

Project notes :

Drawing No : A08

Date : 29/09/2026

Scale : 1:30

Made by : Стела Попова

Покрития стени и тавани

Ателие Алера 2, Овча купел
46.4 кв.м
Нсв = 260

Позиция	Шпакловка	Подови плочки	Стенни плочки	Декоративни плочки	Декоративна лайсна	Интериорна боя	Преходна лайсна	SPC (вероятно и саморазливна замазка)	Подов перваз
Баня Стени	1.4 кв.м	--	14 кв.м	13 бр.	9 бр.	1.4 кв. м	--	--	--
Баня Таван	3.6 кв.м	--	--	--	--	3.6 кв.м	--	--	--
Баня Под	--	3.6 кв. м	--	--	--	--	1 бр.	--	--
Антре, Кухня, Хол Стени	49.0 кв.м	--	--	--	--	49.0 кв.м	--	--	--
Антре, Кухня, Хол Таван	26.4 кв.м	--	--	--	--	26.4 кв.м	--	--	--
Антре, Кухня, Хол Под	--	--	--	--	--	--	--	26.4 кв.м	13 л.м
Спалня Стени	29.0 кв.м	--	--	--	--	29.0 кв.м	--	--	--
Спалня Таван	12.0 кв. м	--	--	--	--	12.0 кв.м	--	--	--
Спалня Под	--	--	--	--	--	--	--	12.0 кв.м	8 л.м
Общи количества	121.4 кв.м	3.6 кв.м	14 кв.м	13 бр	9 бр.	121.4 кв.м	1 бр	38.4 кв.м	21 л.м

SP interior design
+359 898 24 82 85
contact@stelapopova.com
www.stelapopova.com

Drawing name :
Подови и стенни покрития

Project name :
Ателие Алера 2

Project notes :

Drawing No : A11
Date : 29/09/2026
Scale : 1:30
Made by :