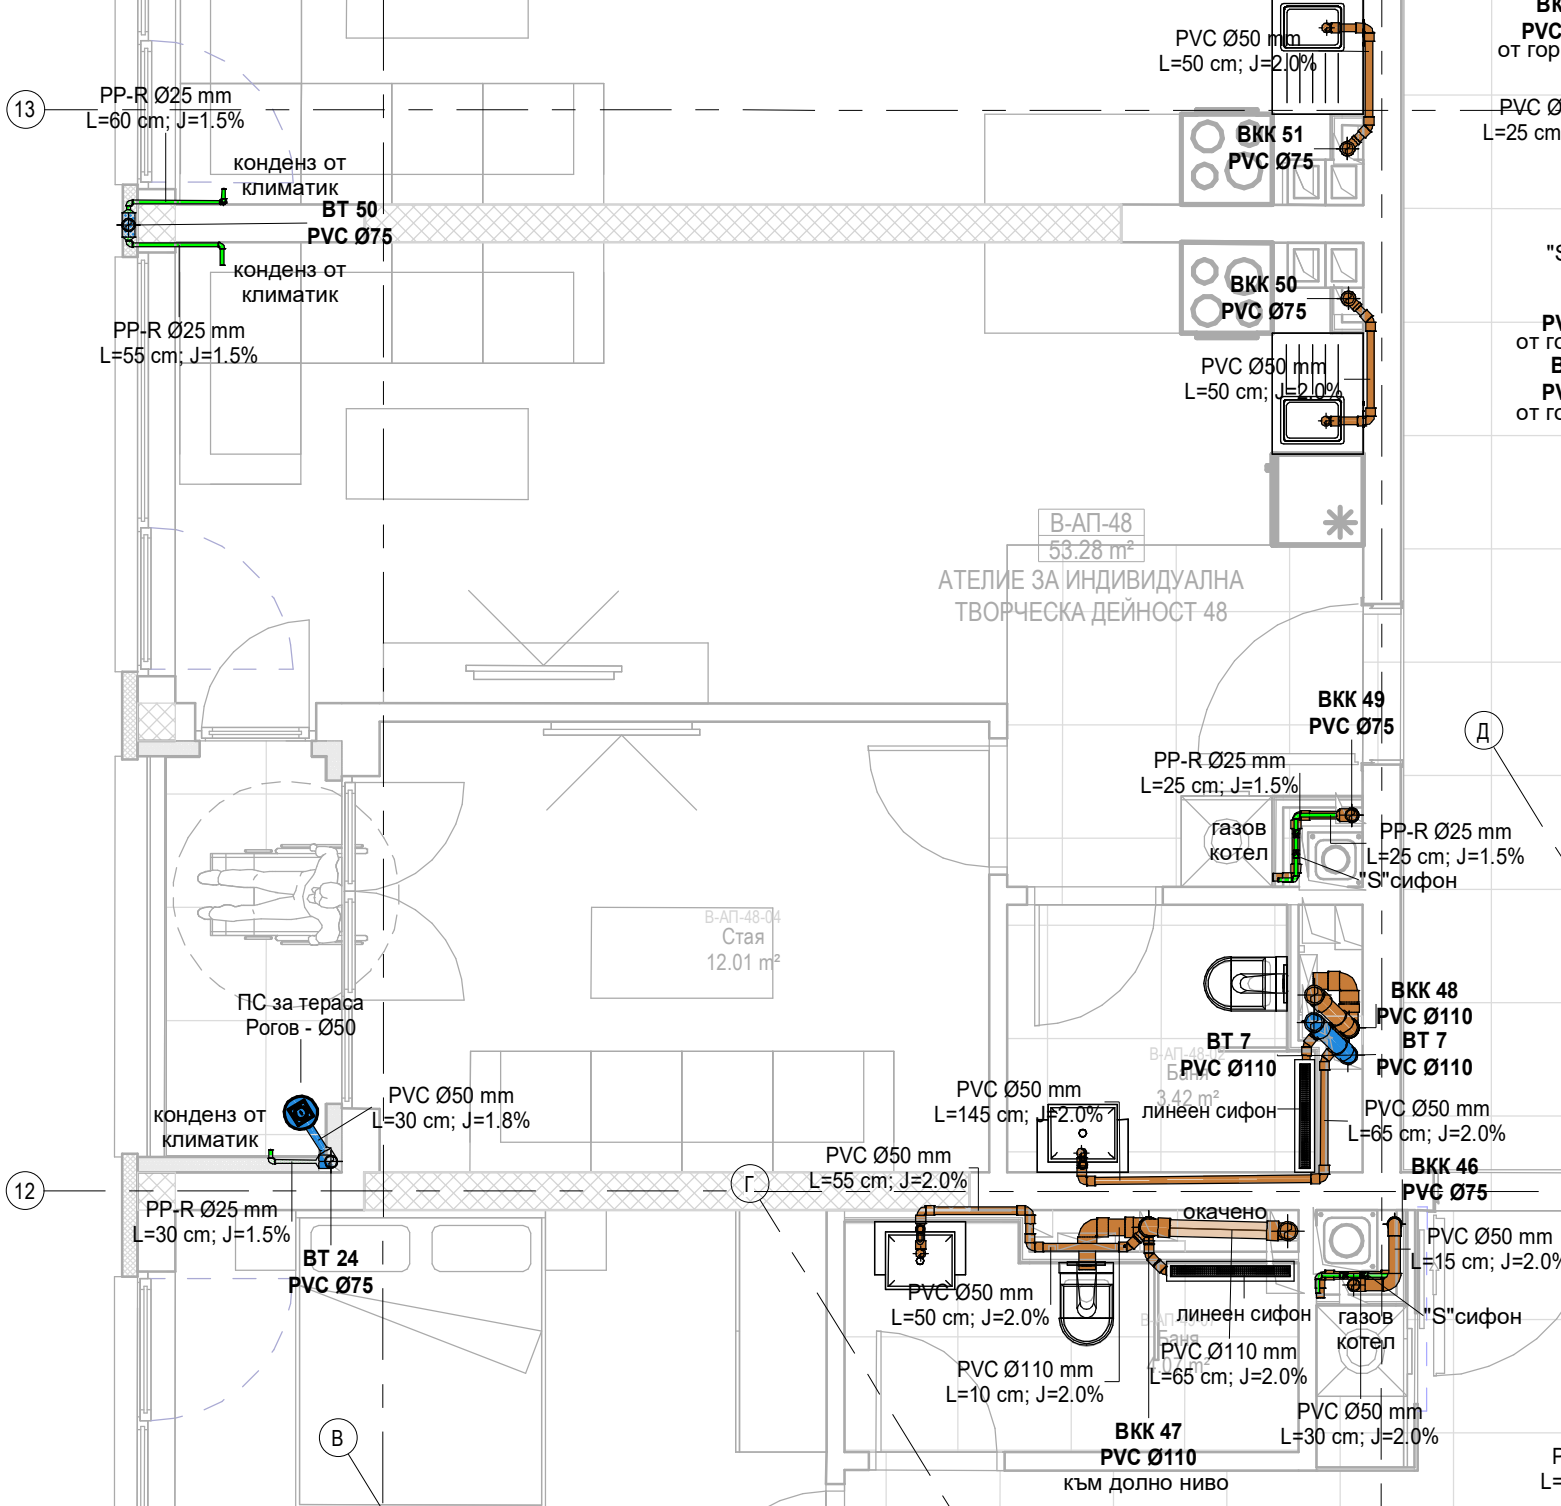

13
PP-R Ø25 mm
L=60 cm; J=1.5%
конденз от
климатик
ВТ 50
PVC Ø75
конденз от
климатик
PP-R Ø25 mm
L=55 cm; J=1.5%
PVC Ø50 mm
L=50 cm; J=2.0%
ВКК 51
PVC Ø75
ВКК 50
PVC Ø75
PVC Ø50 mm
L=50 cm; J=2.0%
В-АП-48
53.28 m²
АТЕЛИЕ ЗА ИНДИВИДУАЛНА
ТВОРЧЕСКА ДЕЙНОСТ 48
ВКК 49
PVC Ø75
PP-R Ø25 mm
L=25 cm; J=1.5%
газов
котел
PP-R Ø25 mm
L=25 cm; J=1.5%
"S"сифон
Д
В-АП-48-04
Стая
12.01 m²
ПС за тераса
Рогов - Ø50
ВКК 48
PVC Ø110
ВТ 7
PVC Ø110
ВТ 7
PVC Ø110
PVC Ø50 mm
L=145 cm; J=2.0%
линеен сифон
PVC Ø50 mm
L=65 cm; J=2.0%
конденз от
климатик
PVC Ø50 mm
L=30 cm; J=1.8%
PVC Ø50 mm
L=55 cm; J=2.0%
ВКК 46
PVC Ø75
12
Г
PP-R Ø25 mm
L=30 cm; J=1.5%
ВТ 24
PVC Ø75
окачено
PVC Ø50 mm
L=15 cm; J=2.0%
PVC Ø50 mm
L=50 cm; J=2.0%
линеен сифон
газов
котел
"S"сифон
PVC Ø110 mm
L=65 cm; J=2.0%
PVC Ø110 mm
L=10 cm; J=2.0%
PVC Ø50 mm
L=30 cm; J=2.0%
В
ВКК 47
PVC Ø110
към долно ниво