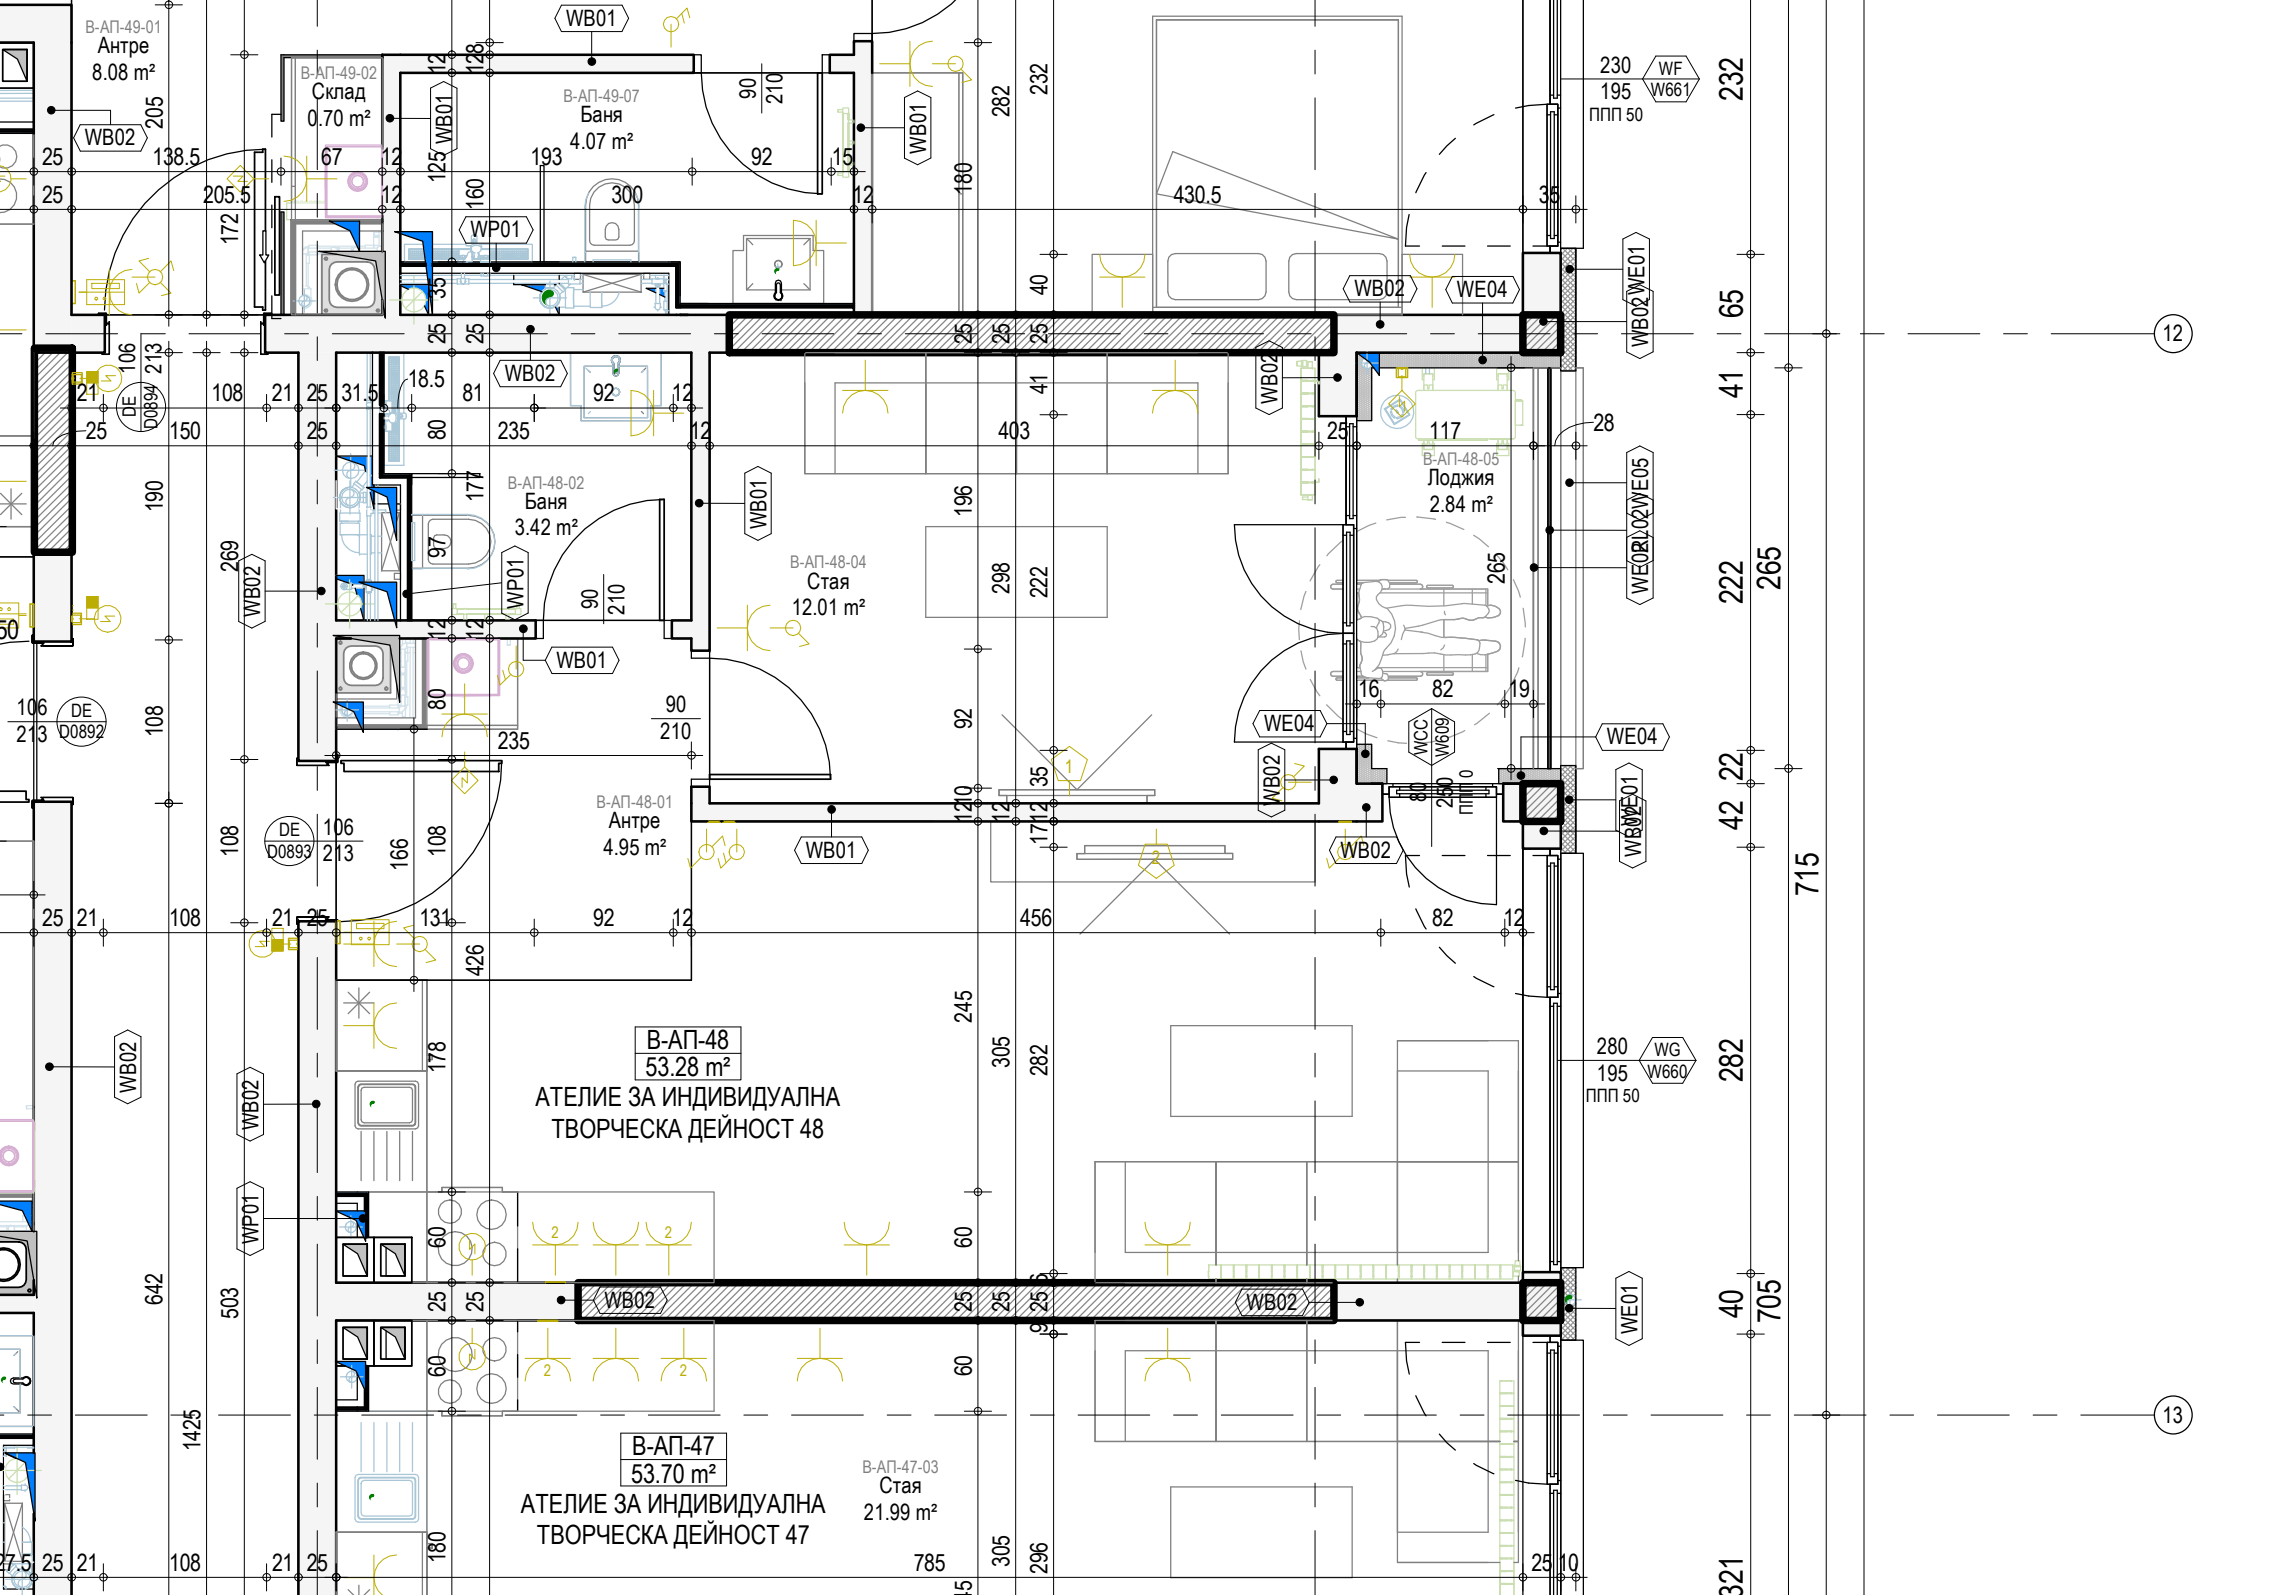

В-АП-49-01
Антре
8.08 m²
В-АП-49-02
Склад
0.70 m²
В-АП-49-07
Баня
4.07 m²
В-АП-48-02
Баня
3.42 m²
В-АП-48-04
Стая
12.01 m²
В-АП-48-05
Лоджия
2.84 m²
В-АП-48-01
Антре
4.95 m²
В-АП-48
53.28 m²
АТЕЛИЕ ЗА ИНДИВИДУАЛНА ТВОРЧЕСКА ДЕЙНОСТ 48
В-АП-47
53.70 m²
АТЕЛИЕ ЗА ИНДИВИДУАЛНА ТВОРЧЕСКА ДЕЙНОСТ 47
В-АП-47-03
Стая
21.99 m²
WB01
WB02
WP01
WE01
WE04
WE05
WF
W661
WG
W660
WCC
W609
DE
D0894
D0892
D0893
ППП 50
12
13