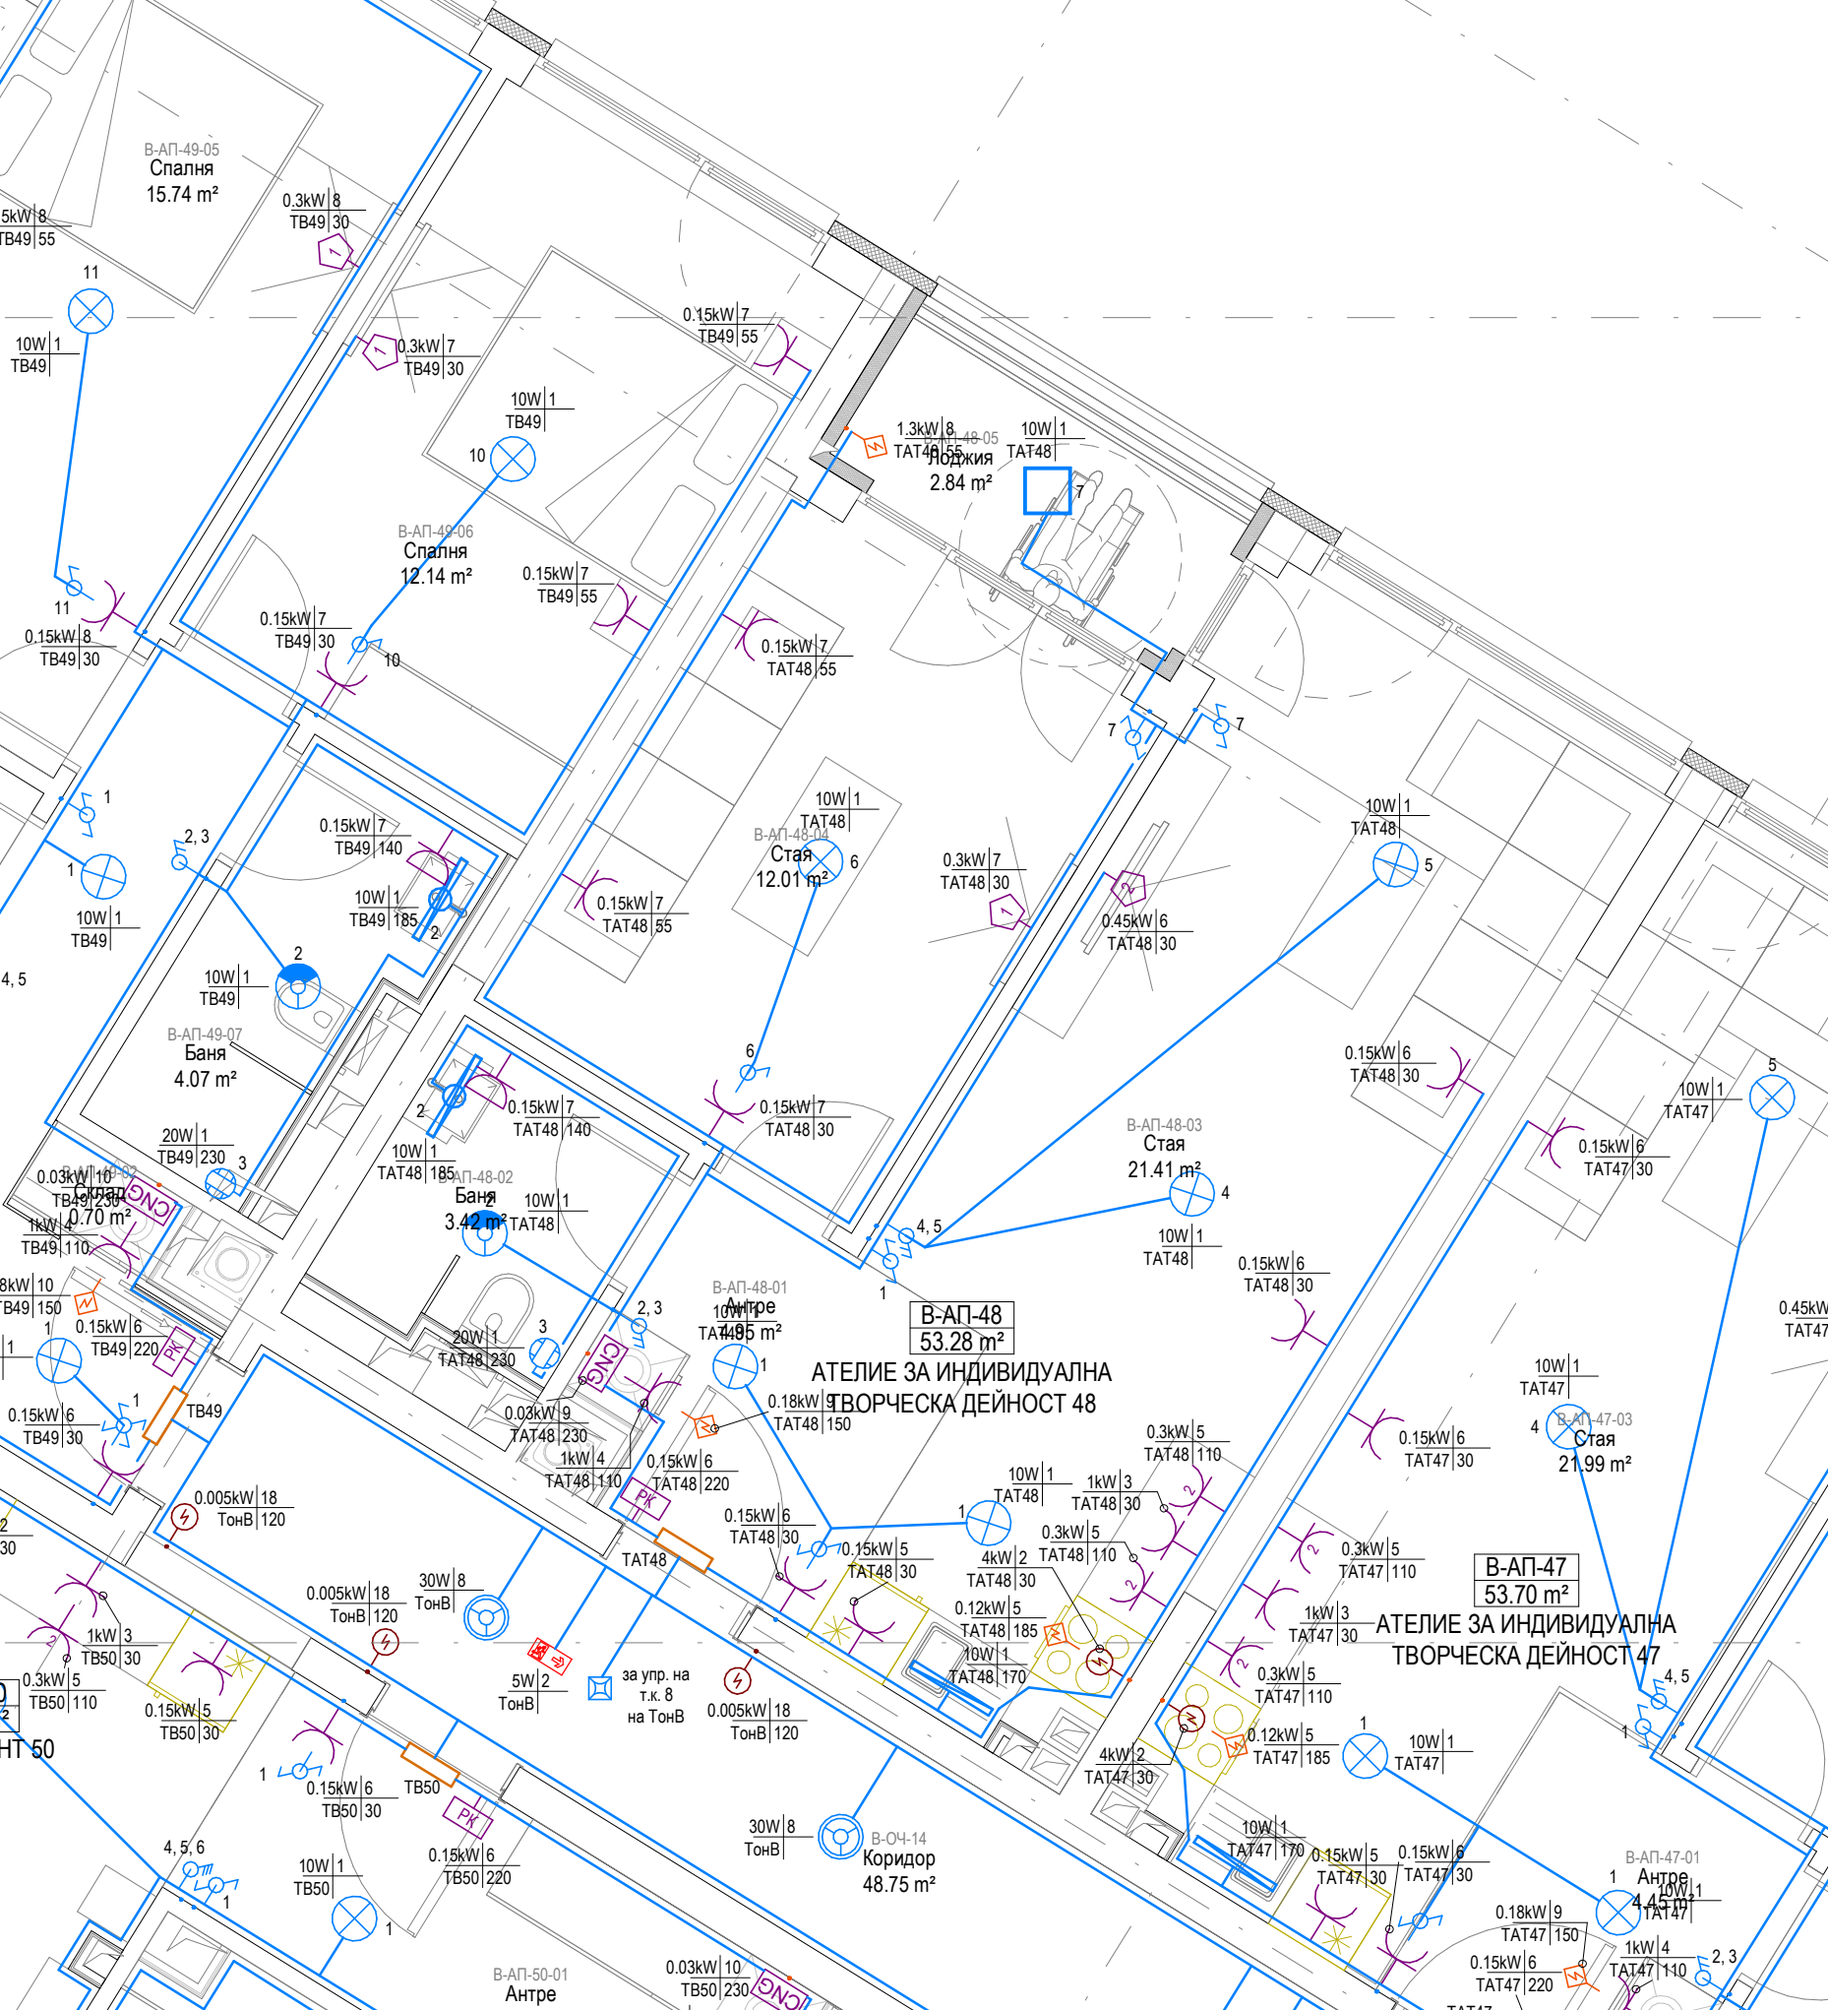

В-АП-49-05
Спалня
15.74 m²
В-АП-49-06
Спалня
12.14 m²
В-АП-48-05
Лоджия
2.84 m²
В-АП-48-04
Стая
12.01 m²
В-АП-49-07
Баня
4.07 m²
В-АП-48-02
Баня
3.42 m²
В-АП-48-03
Стая
21.41 m²
В-АП-48-01
Антре
4.95 m²
В-АП-48
53.28 m²
АТЕЛИЕ ЗА ИНДИВИДУАЛНА ТВОРЧЕСКА ДЕЙНОСТ 48
В-АП-47-03
Стая
21.99 m²
В-АП-47
53.70 m²
АТЕЛИЕ ЗА ИНДИВИДУАЛНА ТВОРЧЕСКА ДЕЙНОСТ 47
В-ОЧ-14
Коридор
48.75 m²
В-АП-47-01
Антре
4.45 m²
В-АП-50-01
Антре
за упр. на т.к. 8 на ТонВ