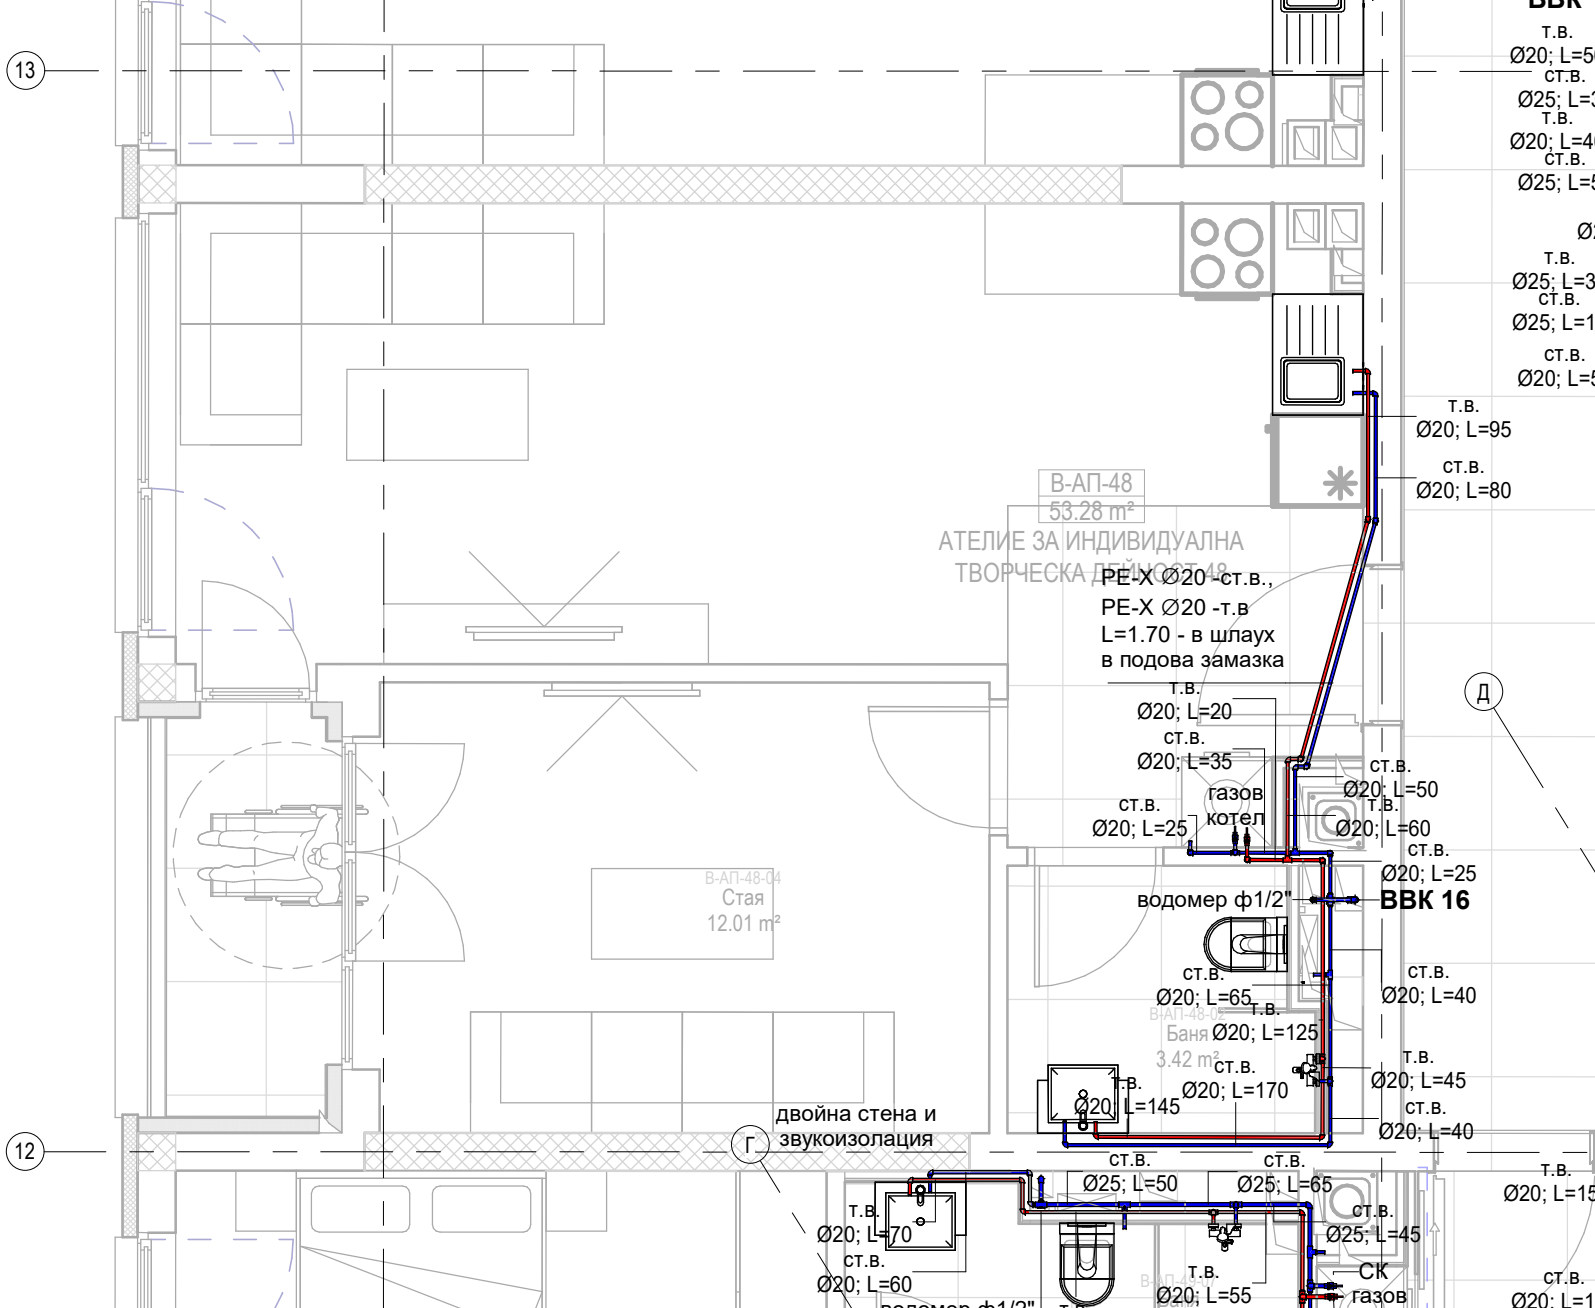

13
12
Г
Д
В-АП-48
53.28 m²
АТЕЛИЕ ЗА ИНДИВИДУАЛНА
ТВОРЧЕСКА ДЕЙНОСТ 48
В-АП-48-04
Стая
12.01 m²
В-АП-48-05
Баня
3.42 m²
PE-X Ø20 -ст.в.,
PE-X Ø20 -т.в
L=1.70 - в шлаух
в подова замазка
газов
котел
водомер ф1/2"
ВВК 16
двойна стена и
звукоизолация
СК
газов
Т.В.
Ø20; L=95
СТ.В.
Ø20; L=80
Т.В.
Ø20; L=20
СТ.В.
Ø20; L=35
СТ.В.
Ø20; L=25
СТ.В.
Ø20; L=50
Т.В.
Ø20; L=60
СТ.В.
Ø20; L=25
СТ.В.
Ø20; L=65
Т.В.
Ø20; L=125
СТ.В.
Ø20; L=40
СТ.В.
Ø20; L=170
Т.В.
Ø20; L=45
Т.В.
Ø20
L=145
СТ.В.
Ø20; L=40
СТ.В.
Ø25; L=50
СТ.В.
Ø25; L=65
Т.В.
Ø20; L=70
СТ.В.
Ø20; L=60
СТ.В.
Ø25; L=45
Т.В.
Ø20; L=55
Т.В.
Ø20; L=15
СТ.В.
Ø20; L=1